




UW PARTNER VOOR
BOUWPROJECTEN

3131 JM26-020

Vloeren Texel de Cocksdorp

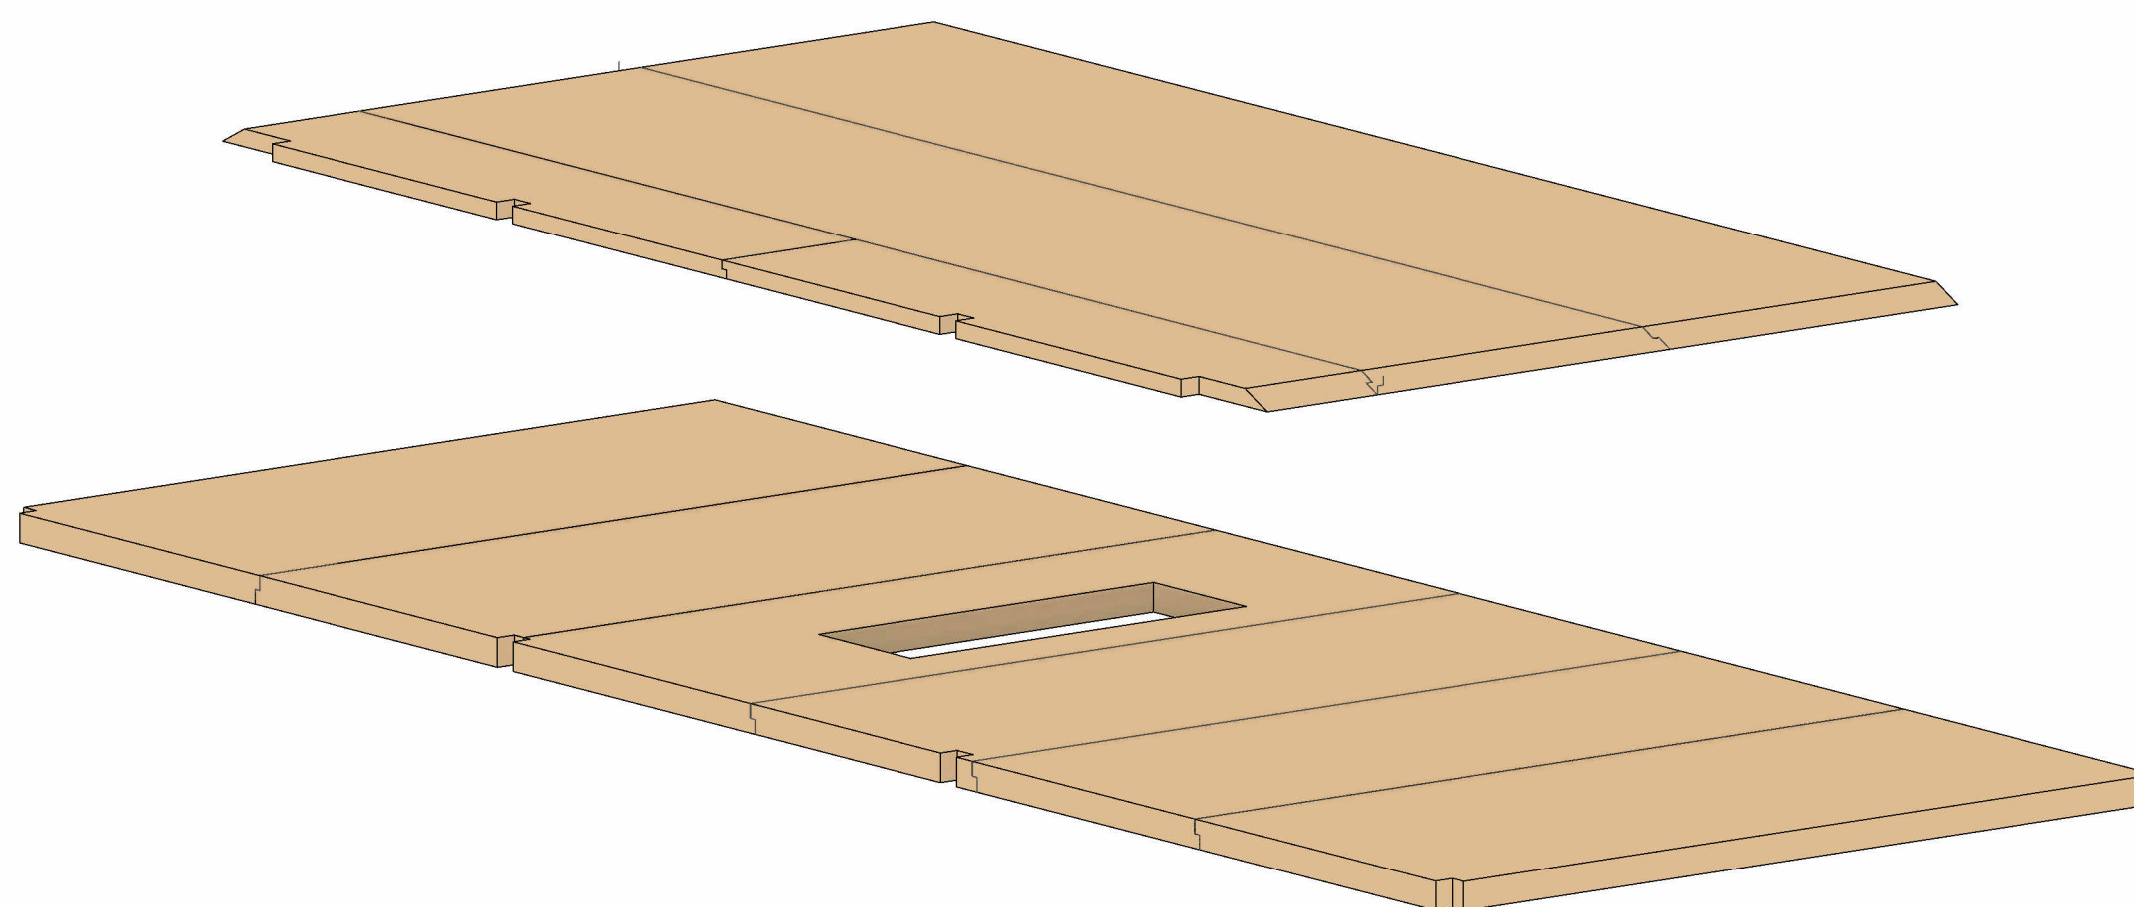



Als organisatie zijn onze kernwaarden duurzaam, innovatief, aansprekend, spraakmakend en meedenkend.

Met meer dan 30 jaar ervaring in het managen van bouwprojecten denken wij graag al in het voortraject van de bouw met u mee.


Naast het leveren van de CLT panelen kunnen wij deze ook monteren, verzorgen wij de engineering en de productietekeningen voor uw project.

WWW.JMCONCEPTEN.NL

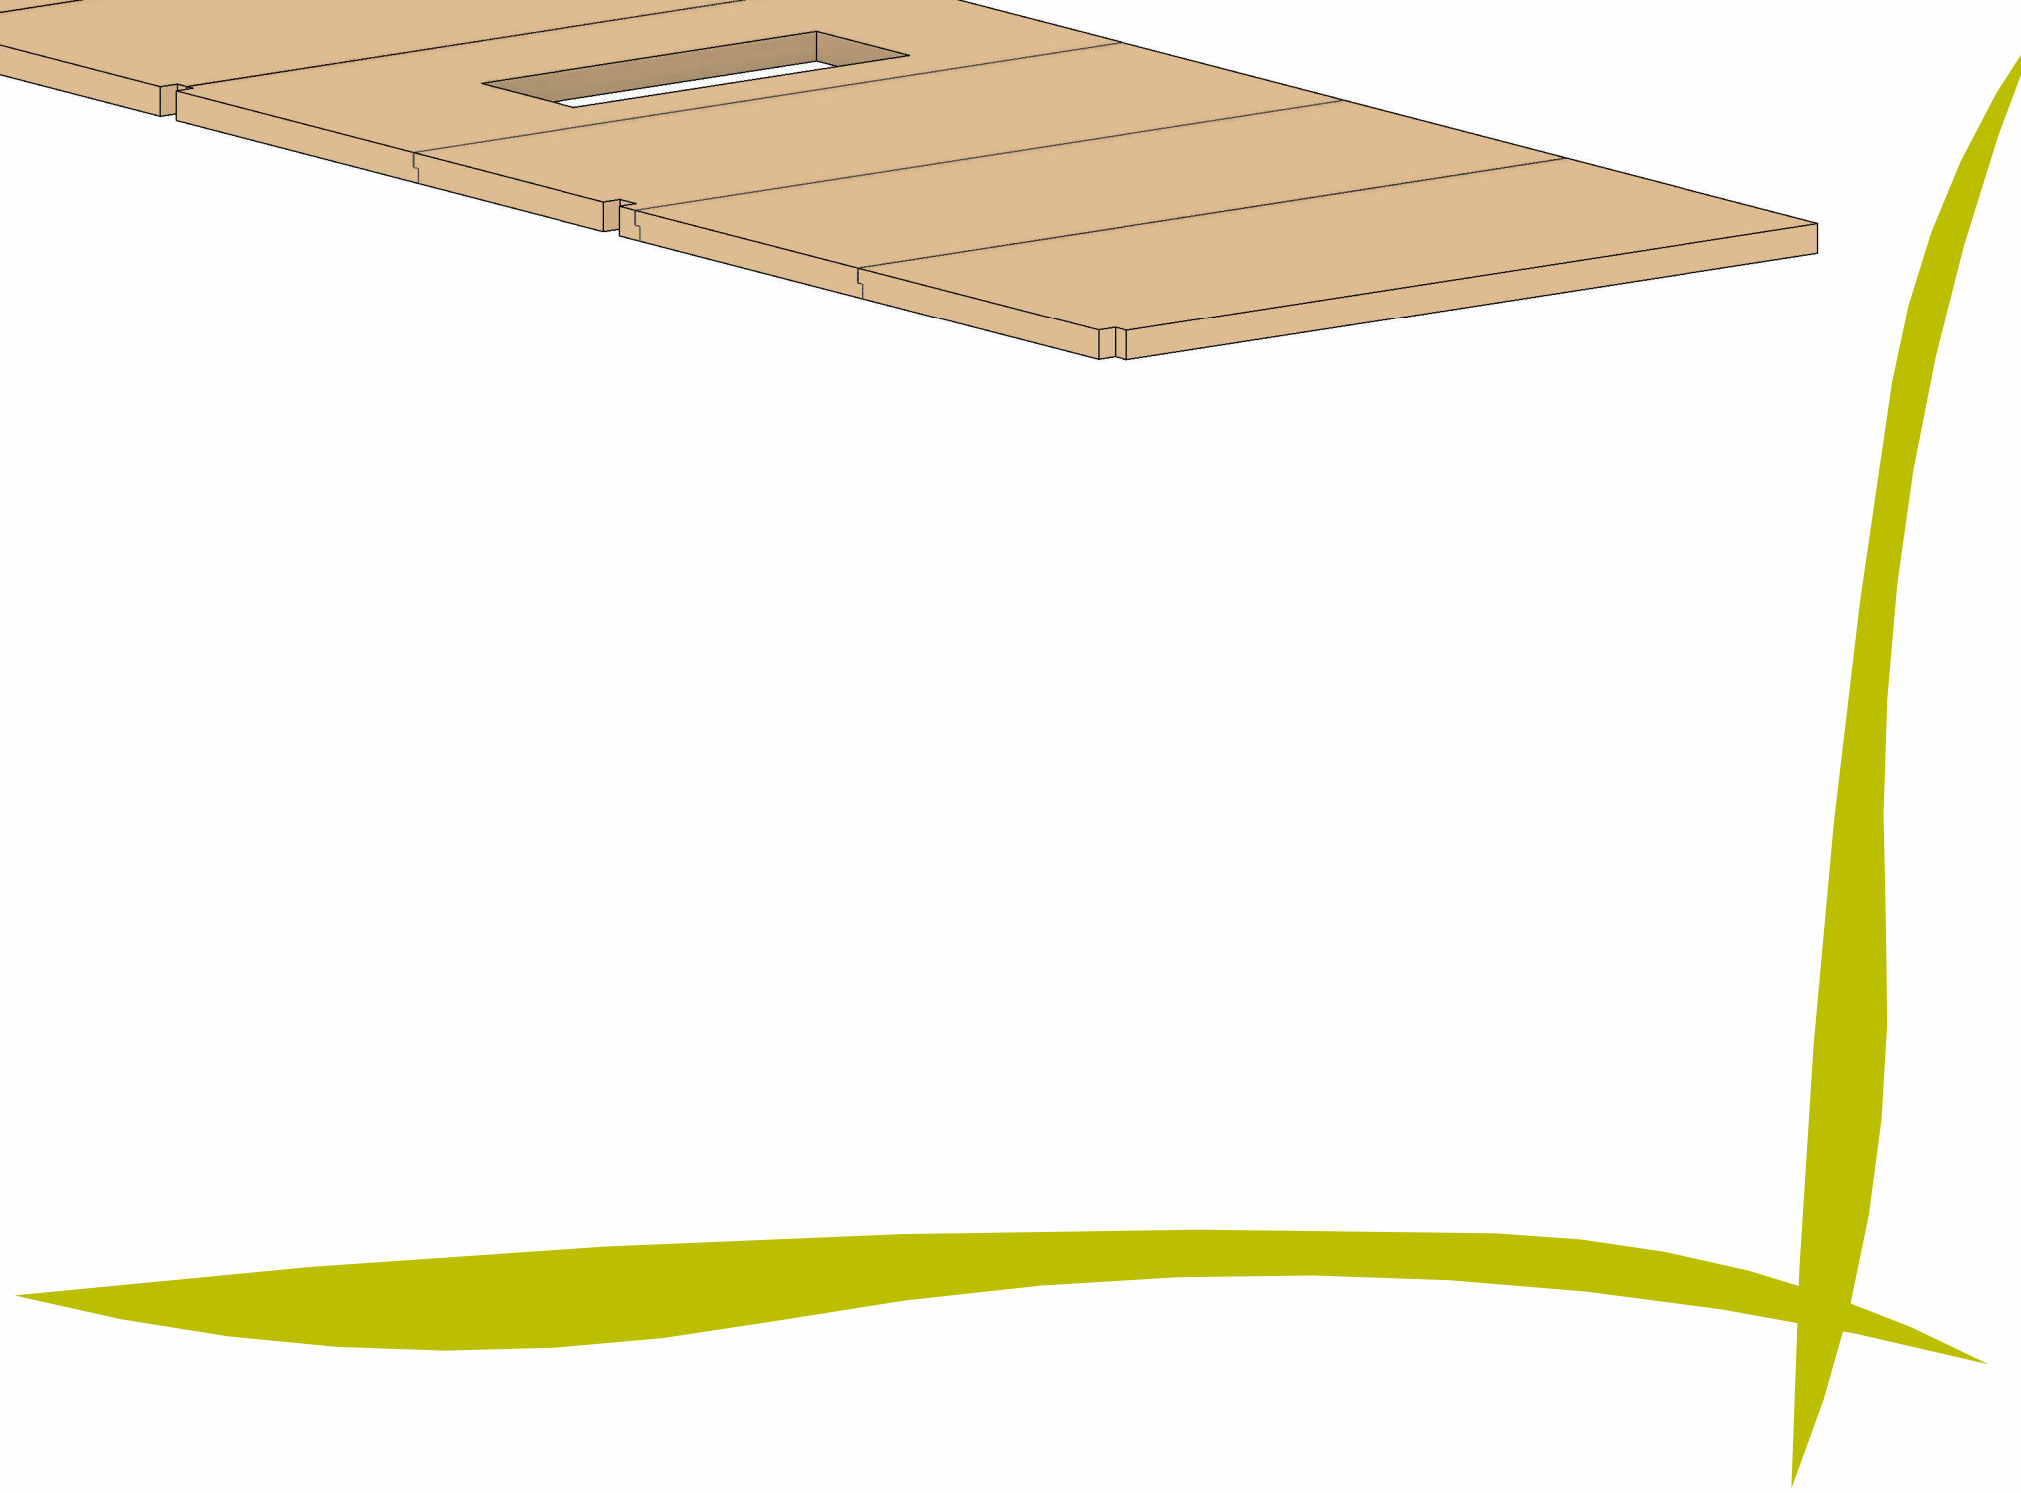

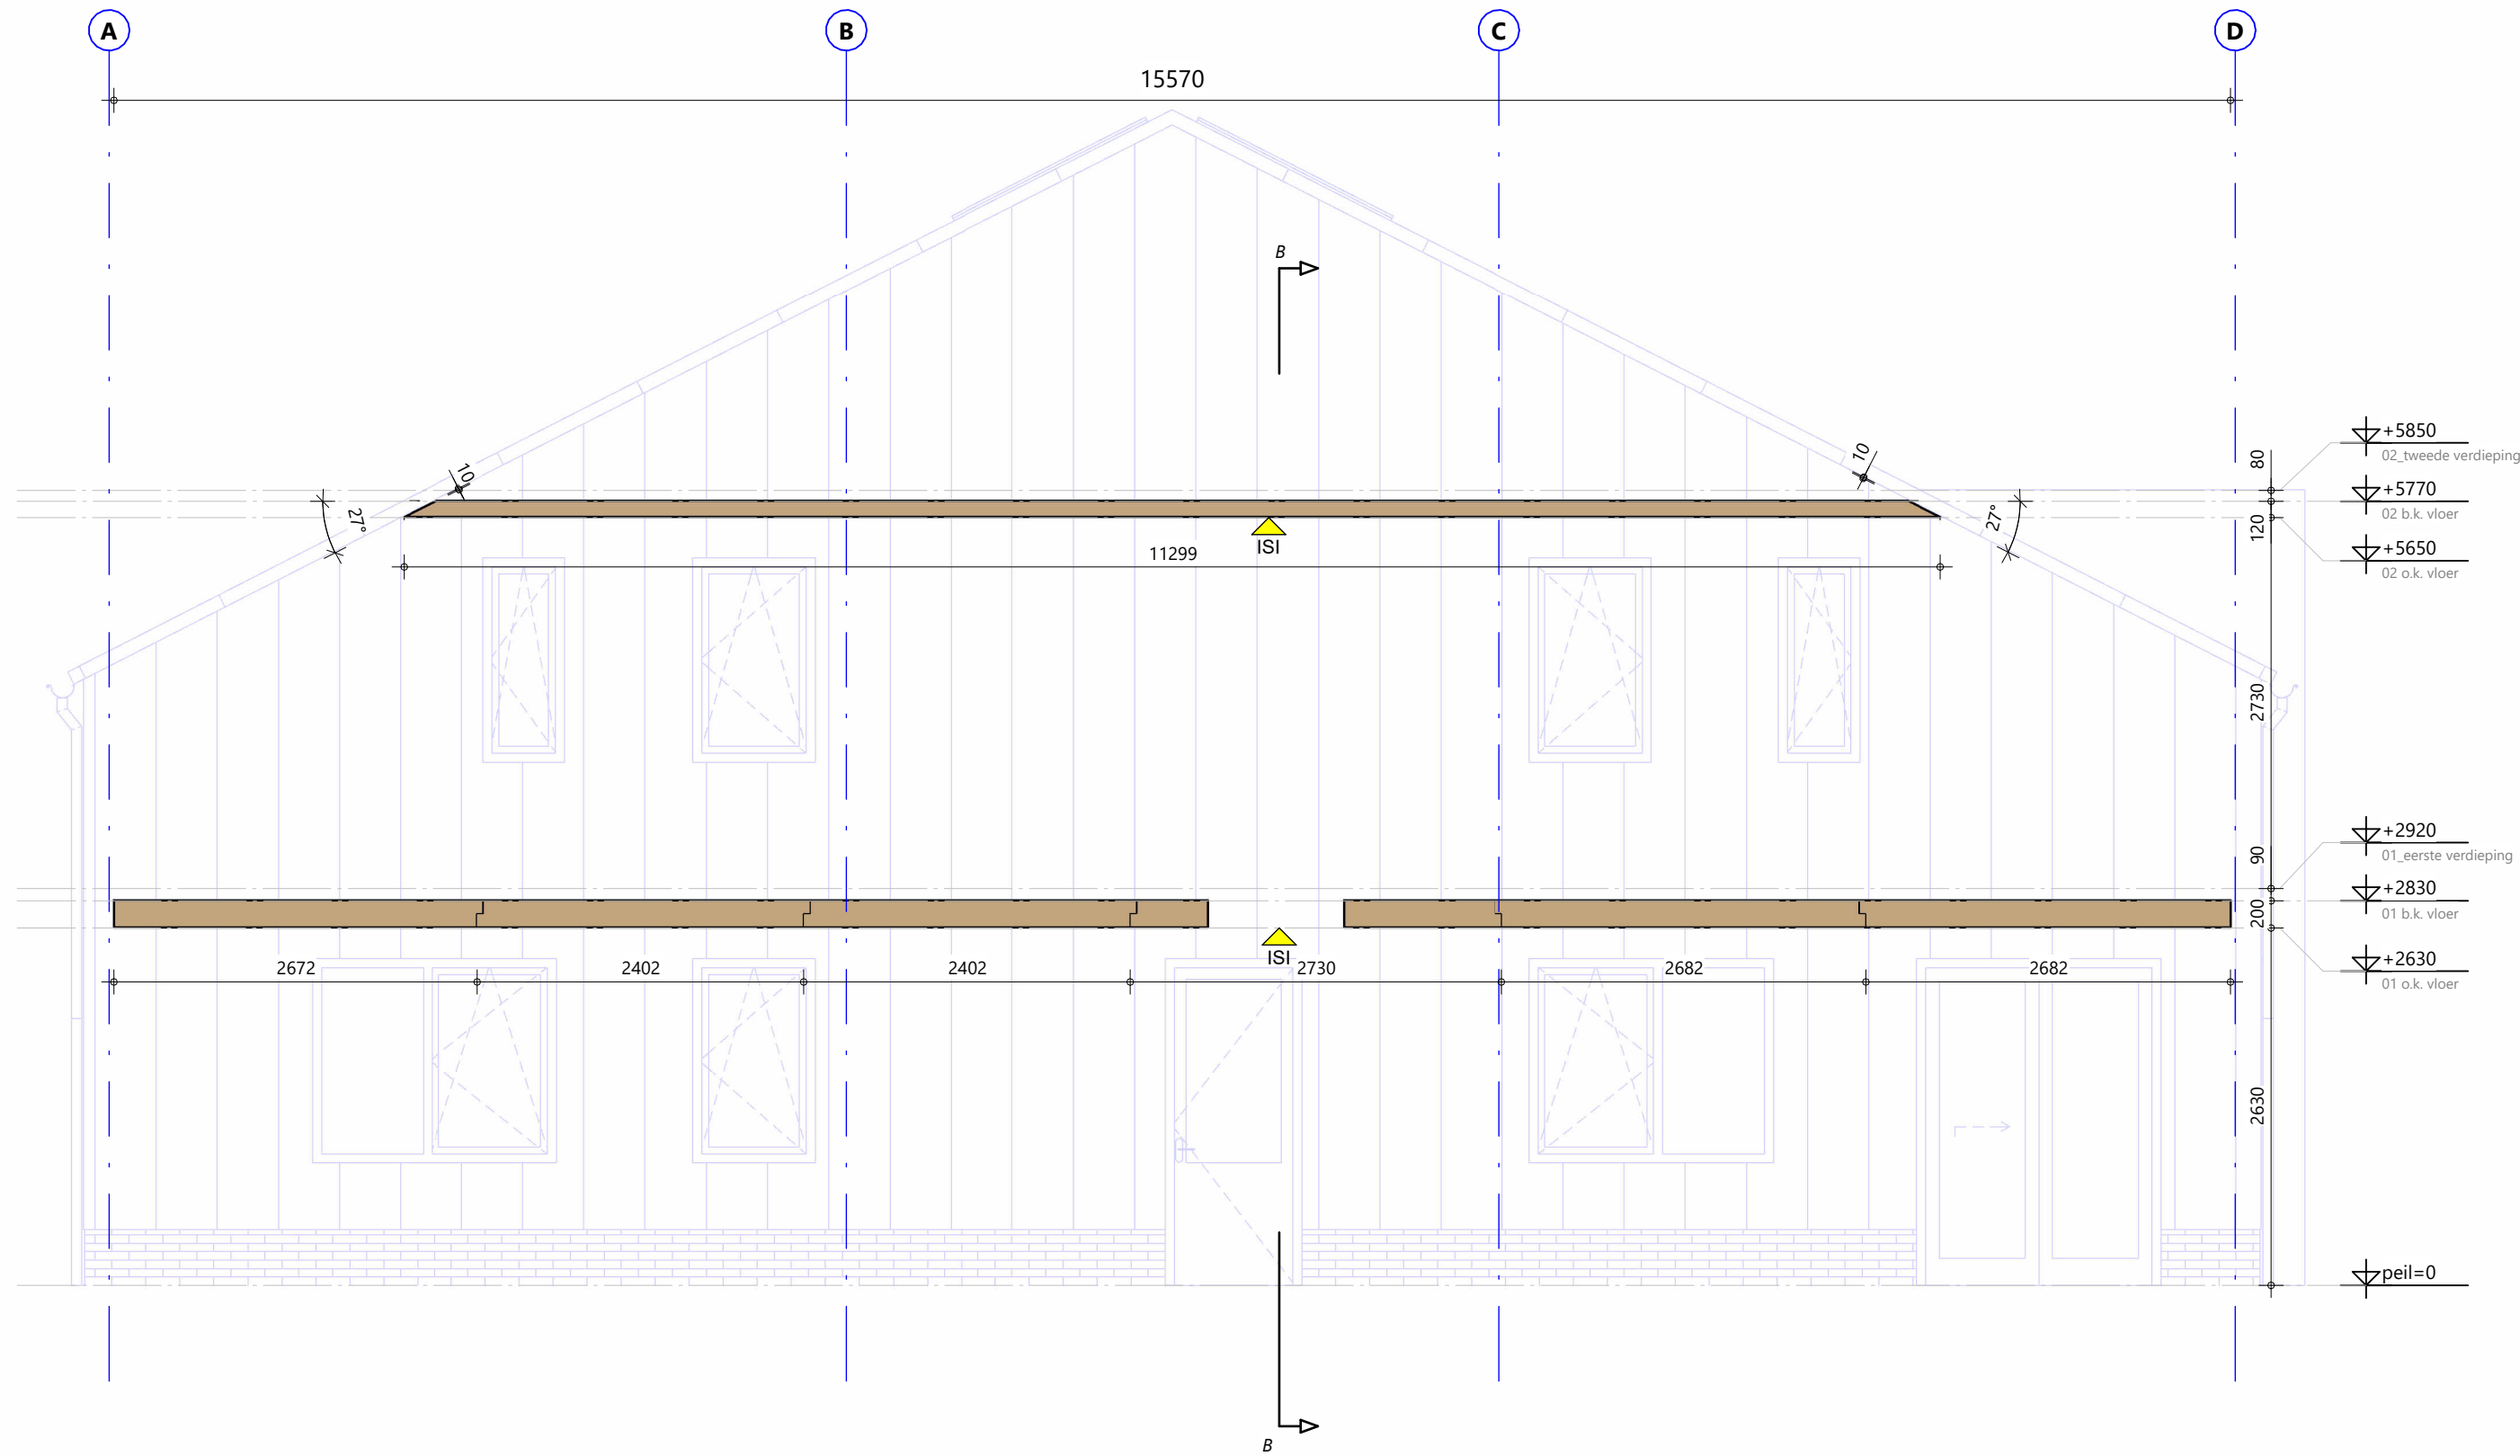

Doorsnede A , Schaal: 1 : 50

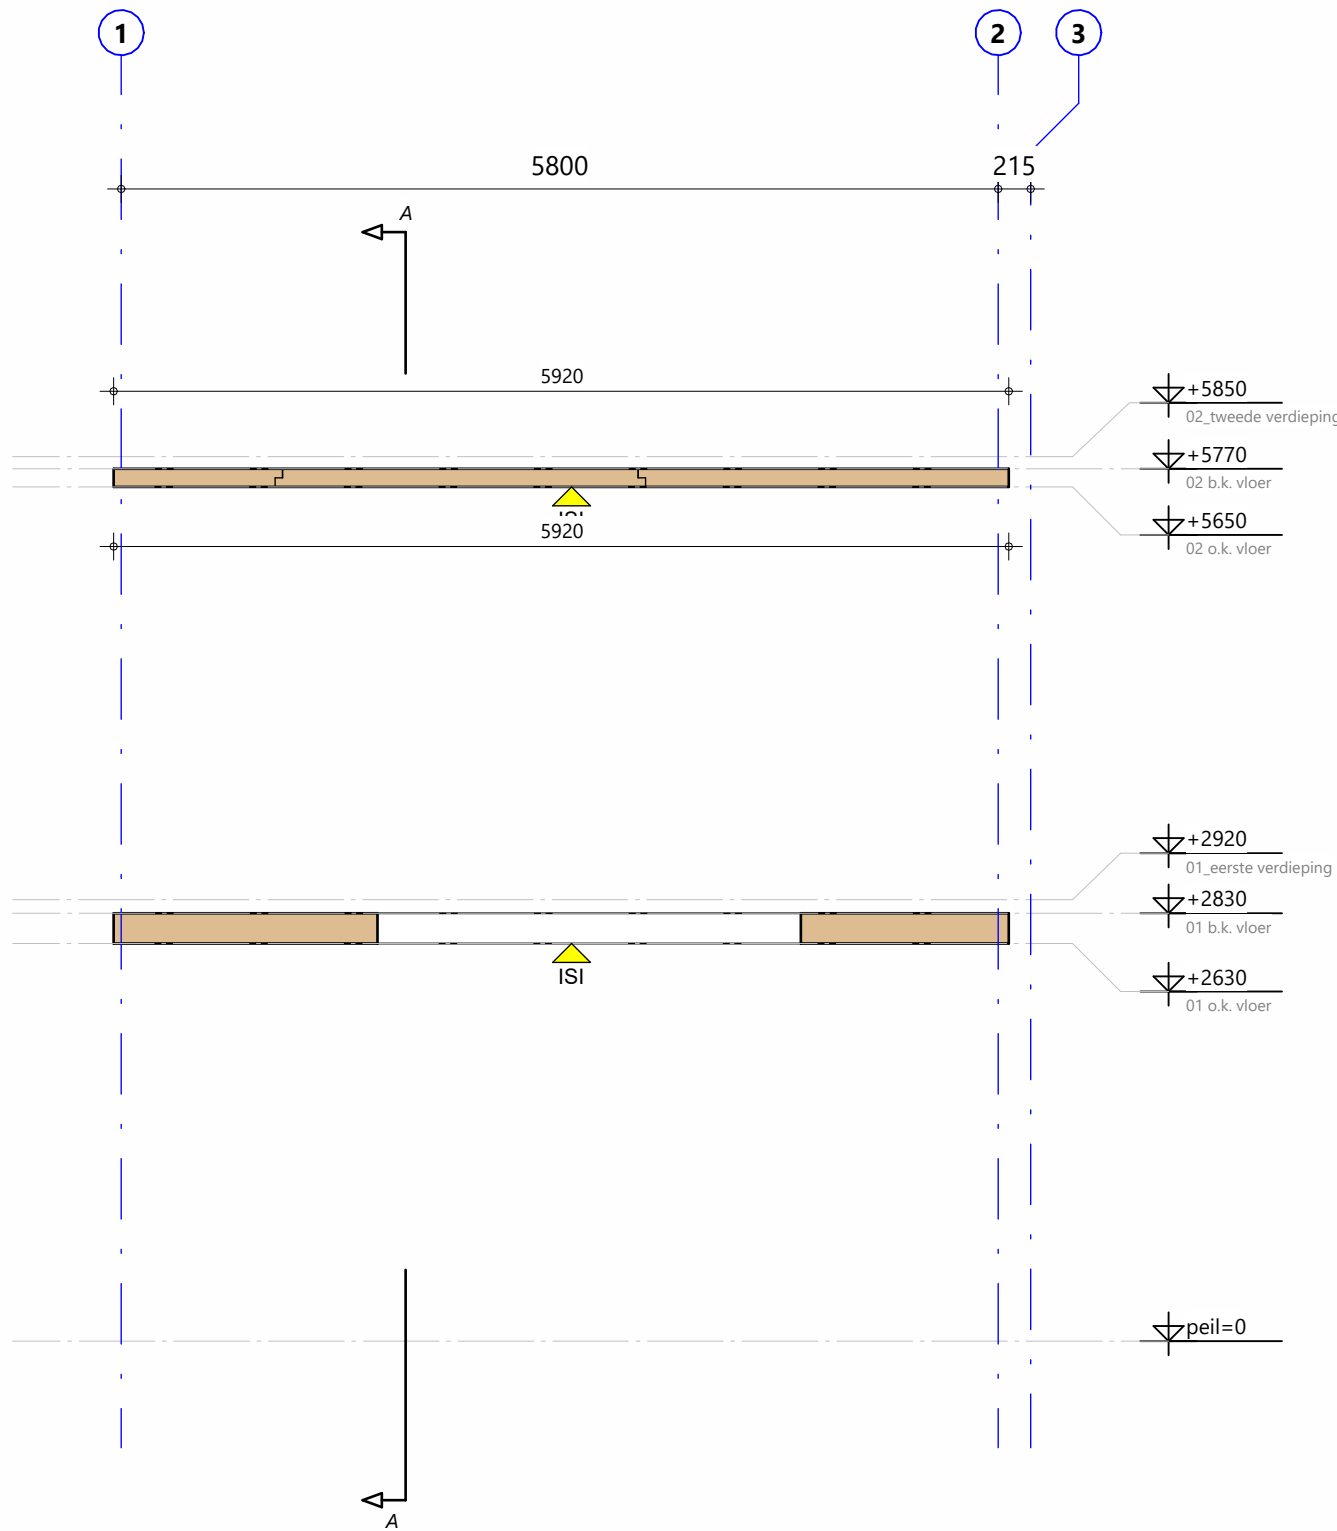

Doorsnede B , Schaal: 1 : 50



Sophialaan 7a
3542 AR Utrecht
T: +31 (0) 73 644 7500
E: info@jmconcepten.nl

Doorsnedes


Vloeren Texel
Krimweg 53, de Cocksdorp

Opdrachtgever:


Projectnr: 3131
Fase:
Auteur: PMol

Formaat: A2
Schaal:
1^e datum: 04-05-2026
Status:
Tekeningnr: CLTD-01

Tekening ongeschikt voor uitvoeringsfase
Geprint 4-5-2026 14:58:53

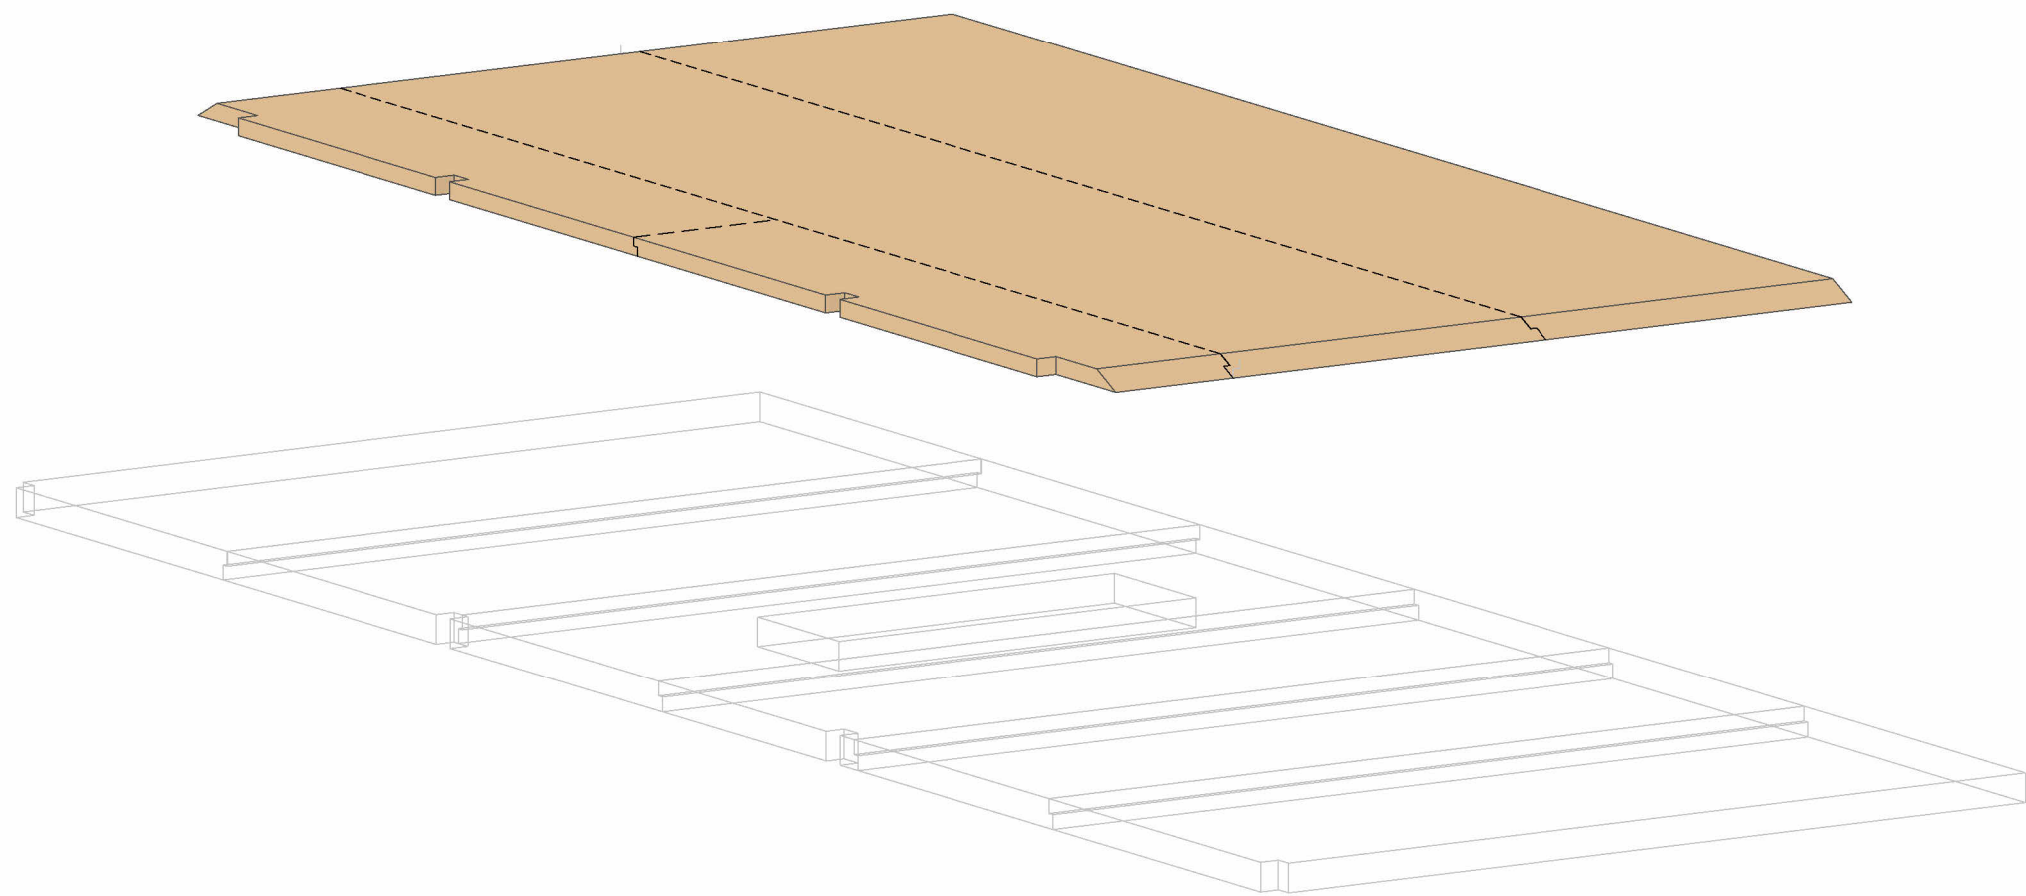

CLT - 120-03s-1-TL

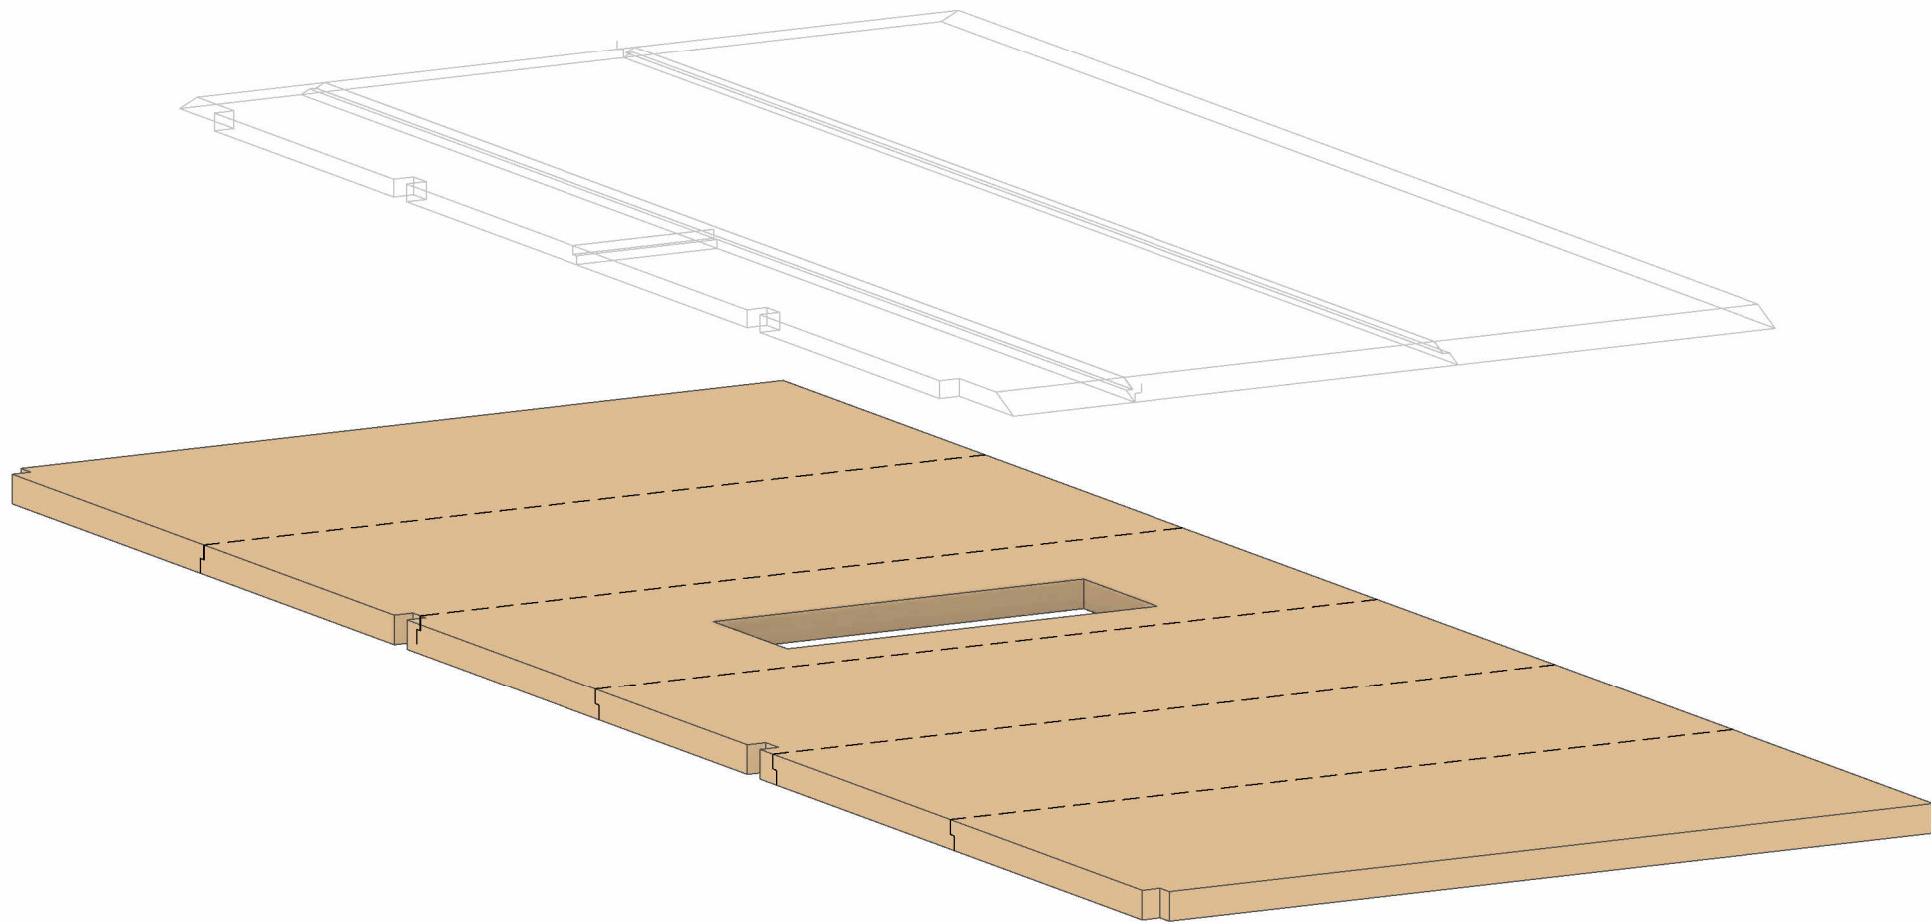

CLT - 200-05s-1-TL



Sophialaan 7a
3542 AR Utrecht
T: +31 (0) 73 644 7500
E: info@jmconcepten.nl


Demarcatie Type Panelen

Vloeren Texel
Krimweg 53, de Cocksdorp

Opdrachtgever:

Projectnr:	3131	Formaat:	A2
Fase:		Schaal:	
Auteur:	PMol	1^e datum:	04-05-2026
		Status:	
		Tekeningnr:	CLTDEM-01

Tekening ongeschikt voor uitvoeringsfase
Geprint 4-5-2026 14:58:57

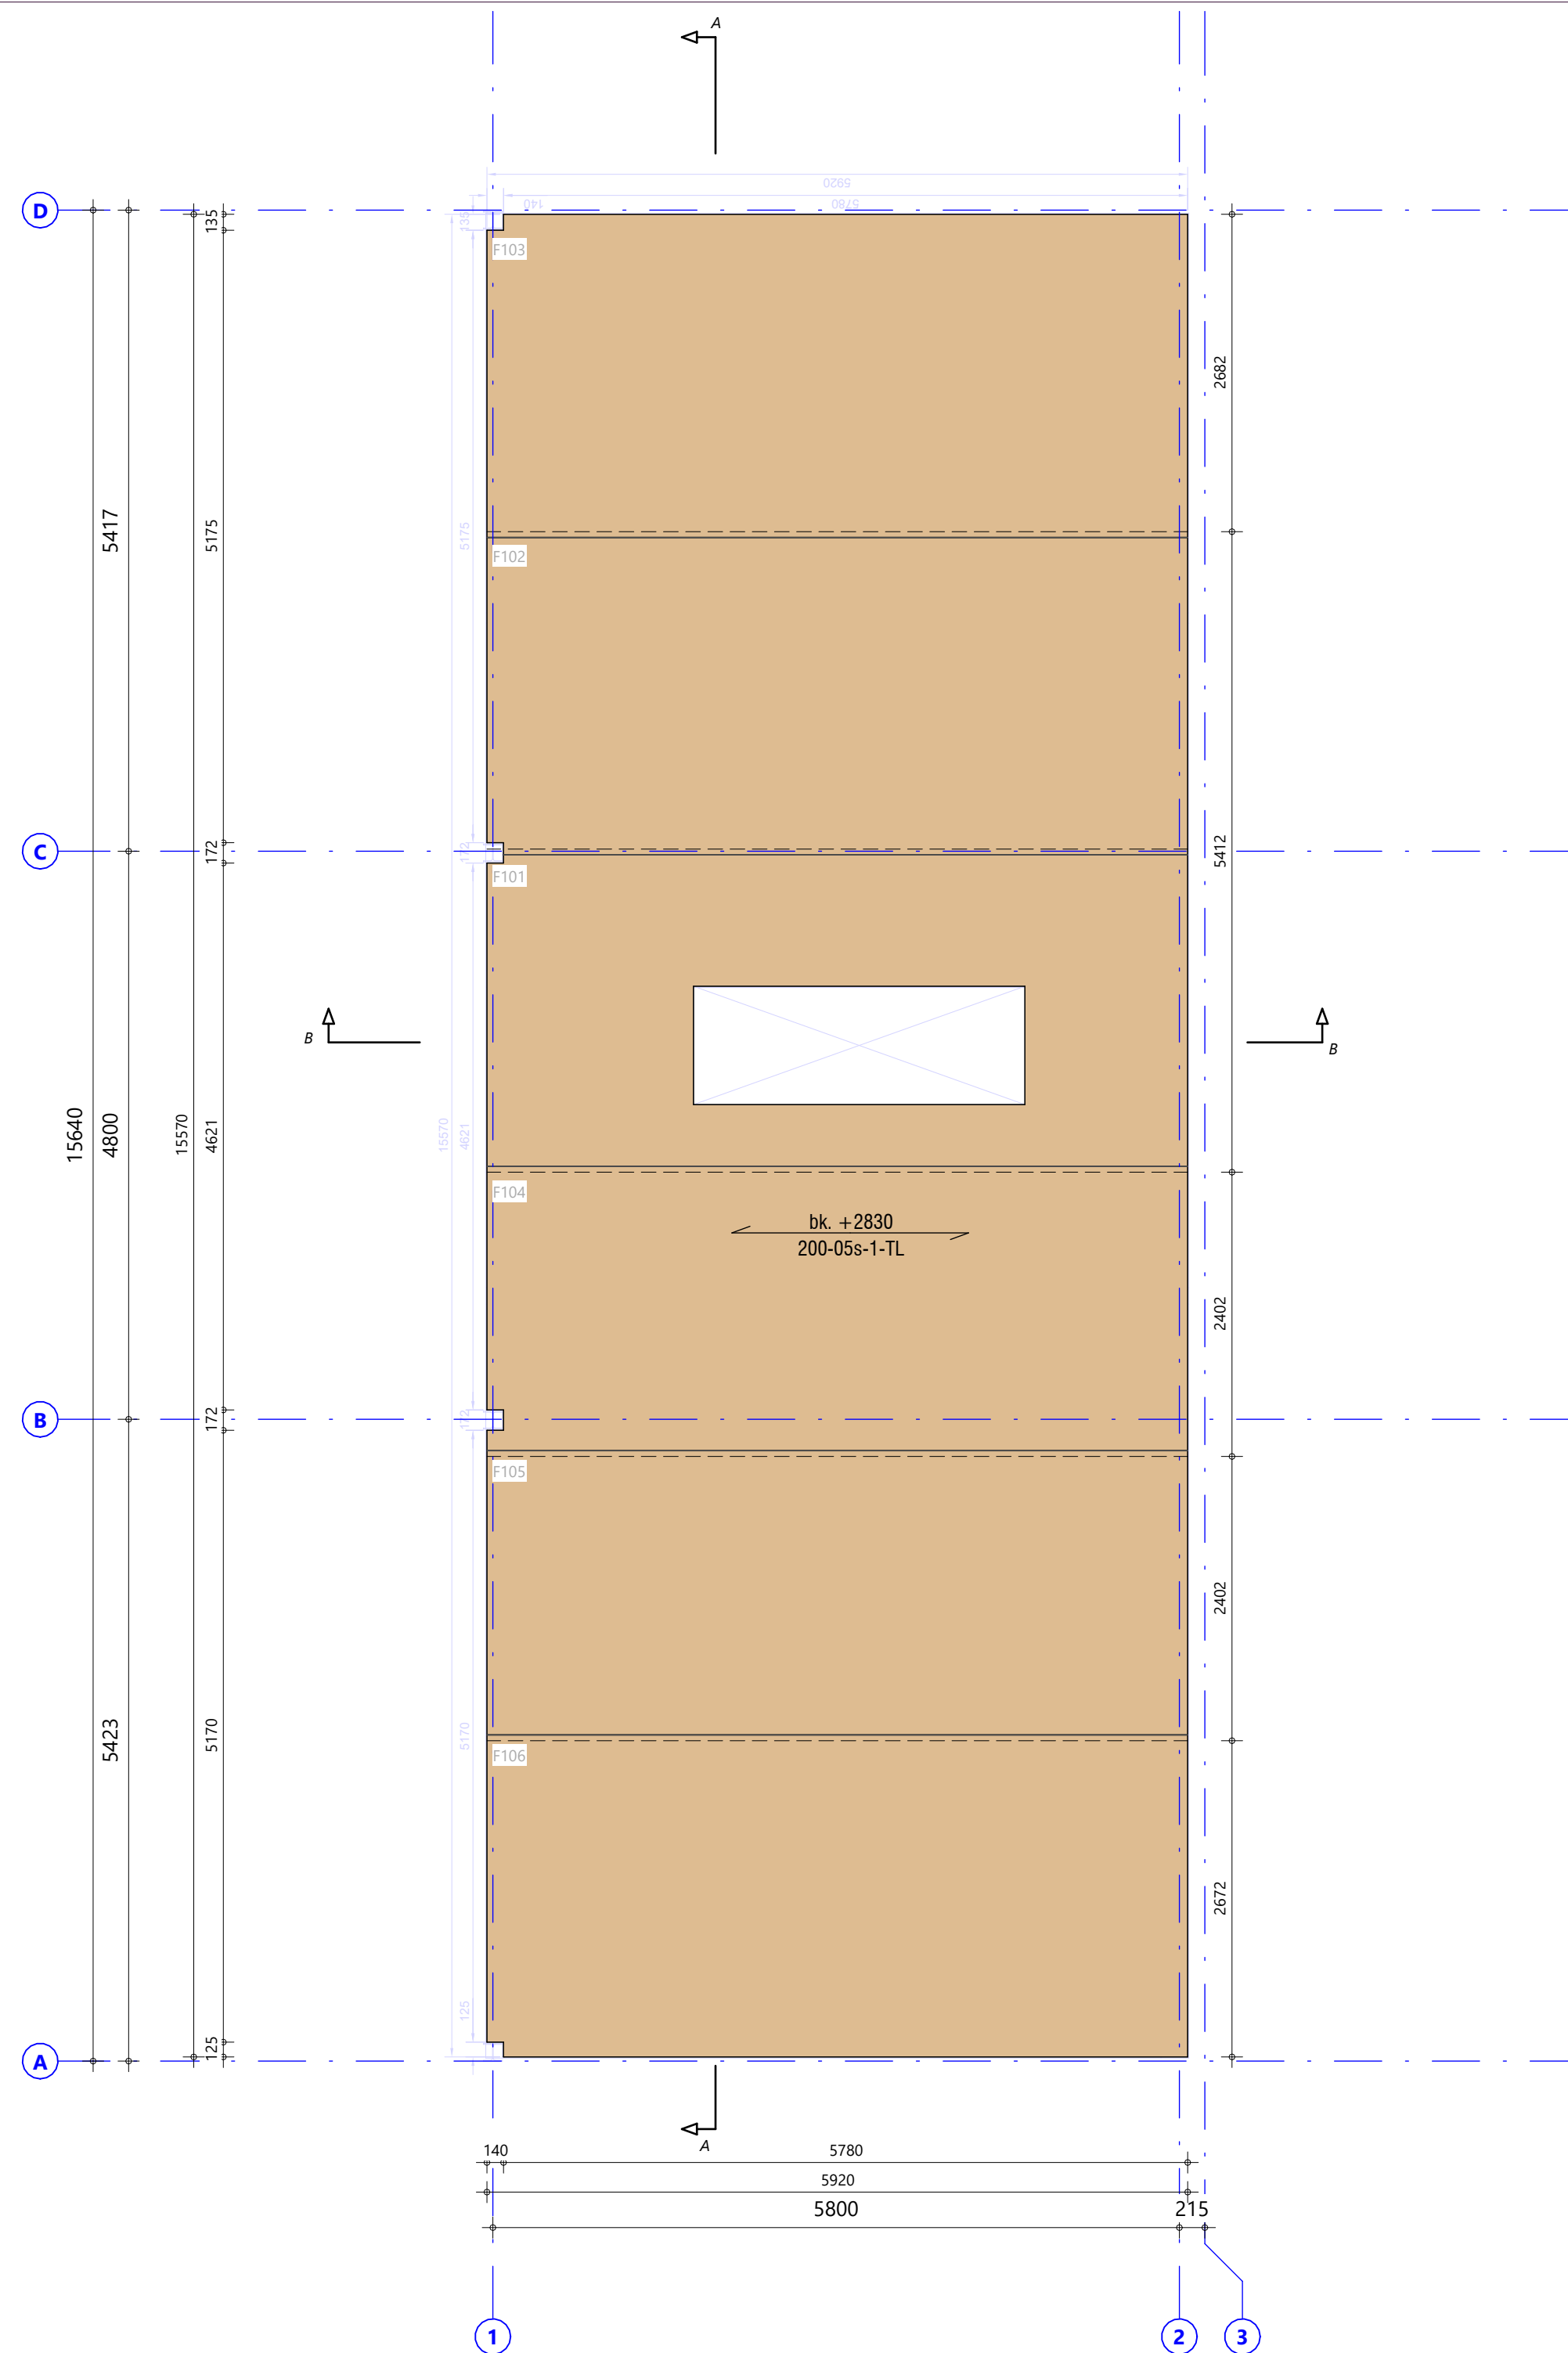

Sophialaan 7a
3542 AR Utrecht
T: +31 (0) 73 644 7500
E: info@jmconcepten.nl

Plattegrond 1e Verdieping


Vloeren Texel
Krimweg 53, de Cocksdorp

Opdrachtgever:

Projectnr: 3131
Fase:
Auteur: PMol

Formaat: A2
Schaal: 1:50
1^e datum: 04-05-2026
Status:
Tekeningnr: CLTP-02

Tekening ongeschikt voor uitvoeringsfase
Geprint 4-5-2026 14:58:57

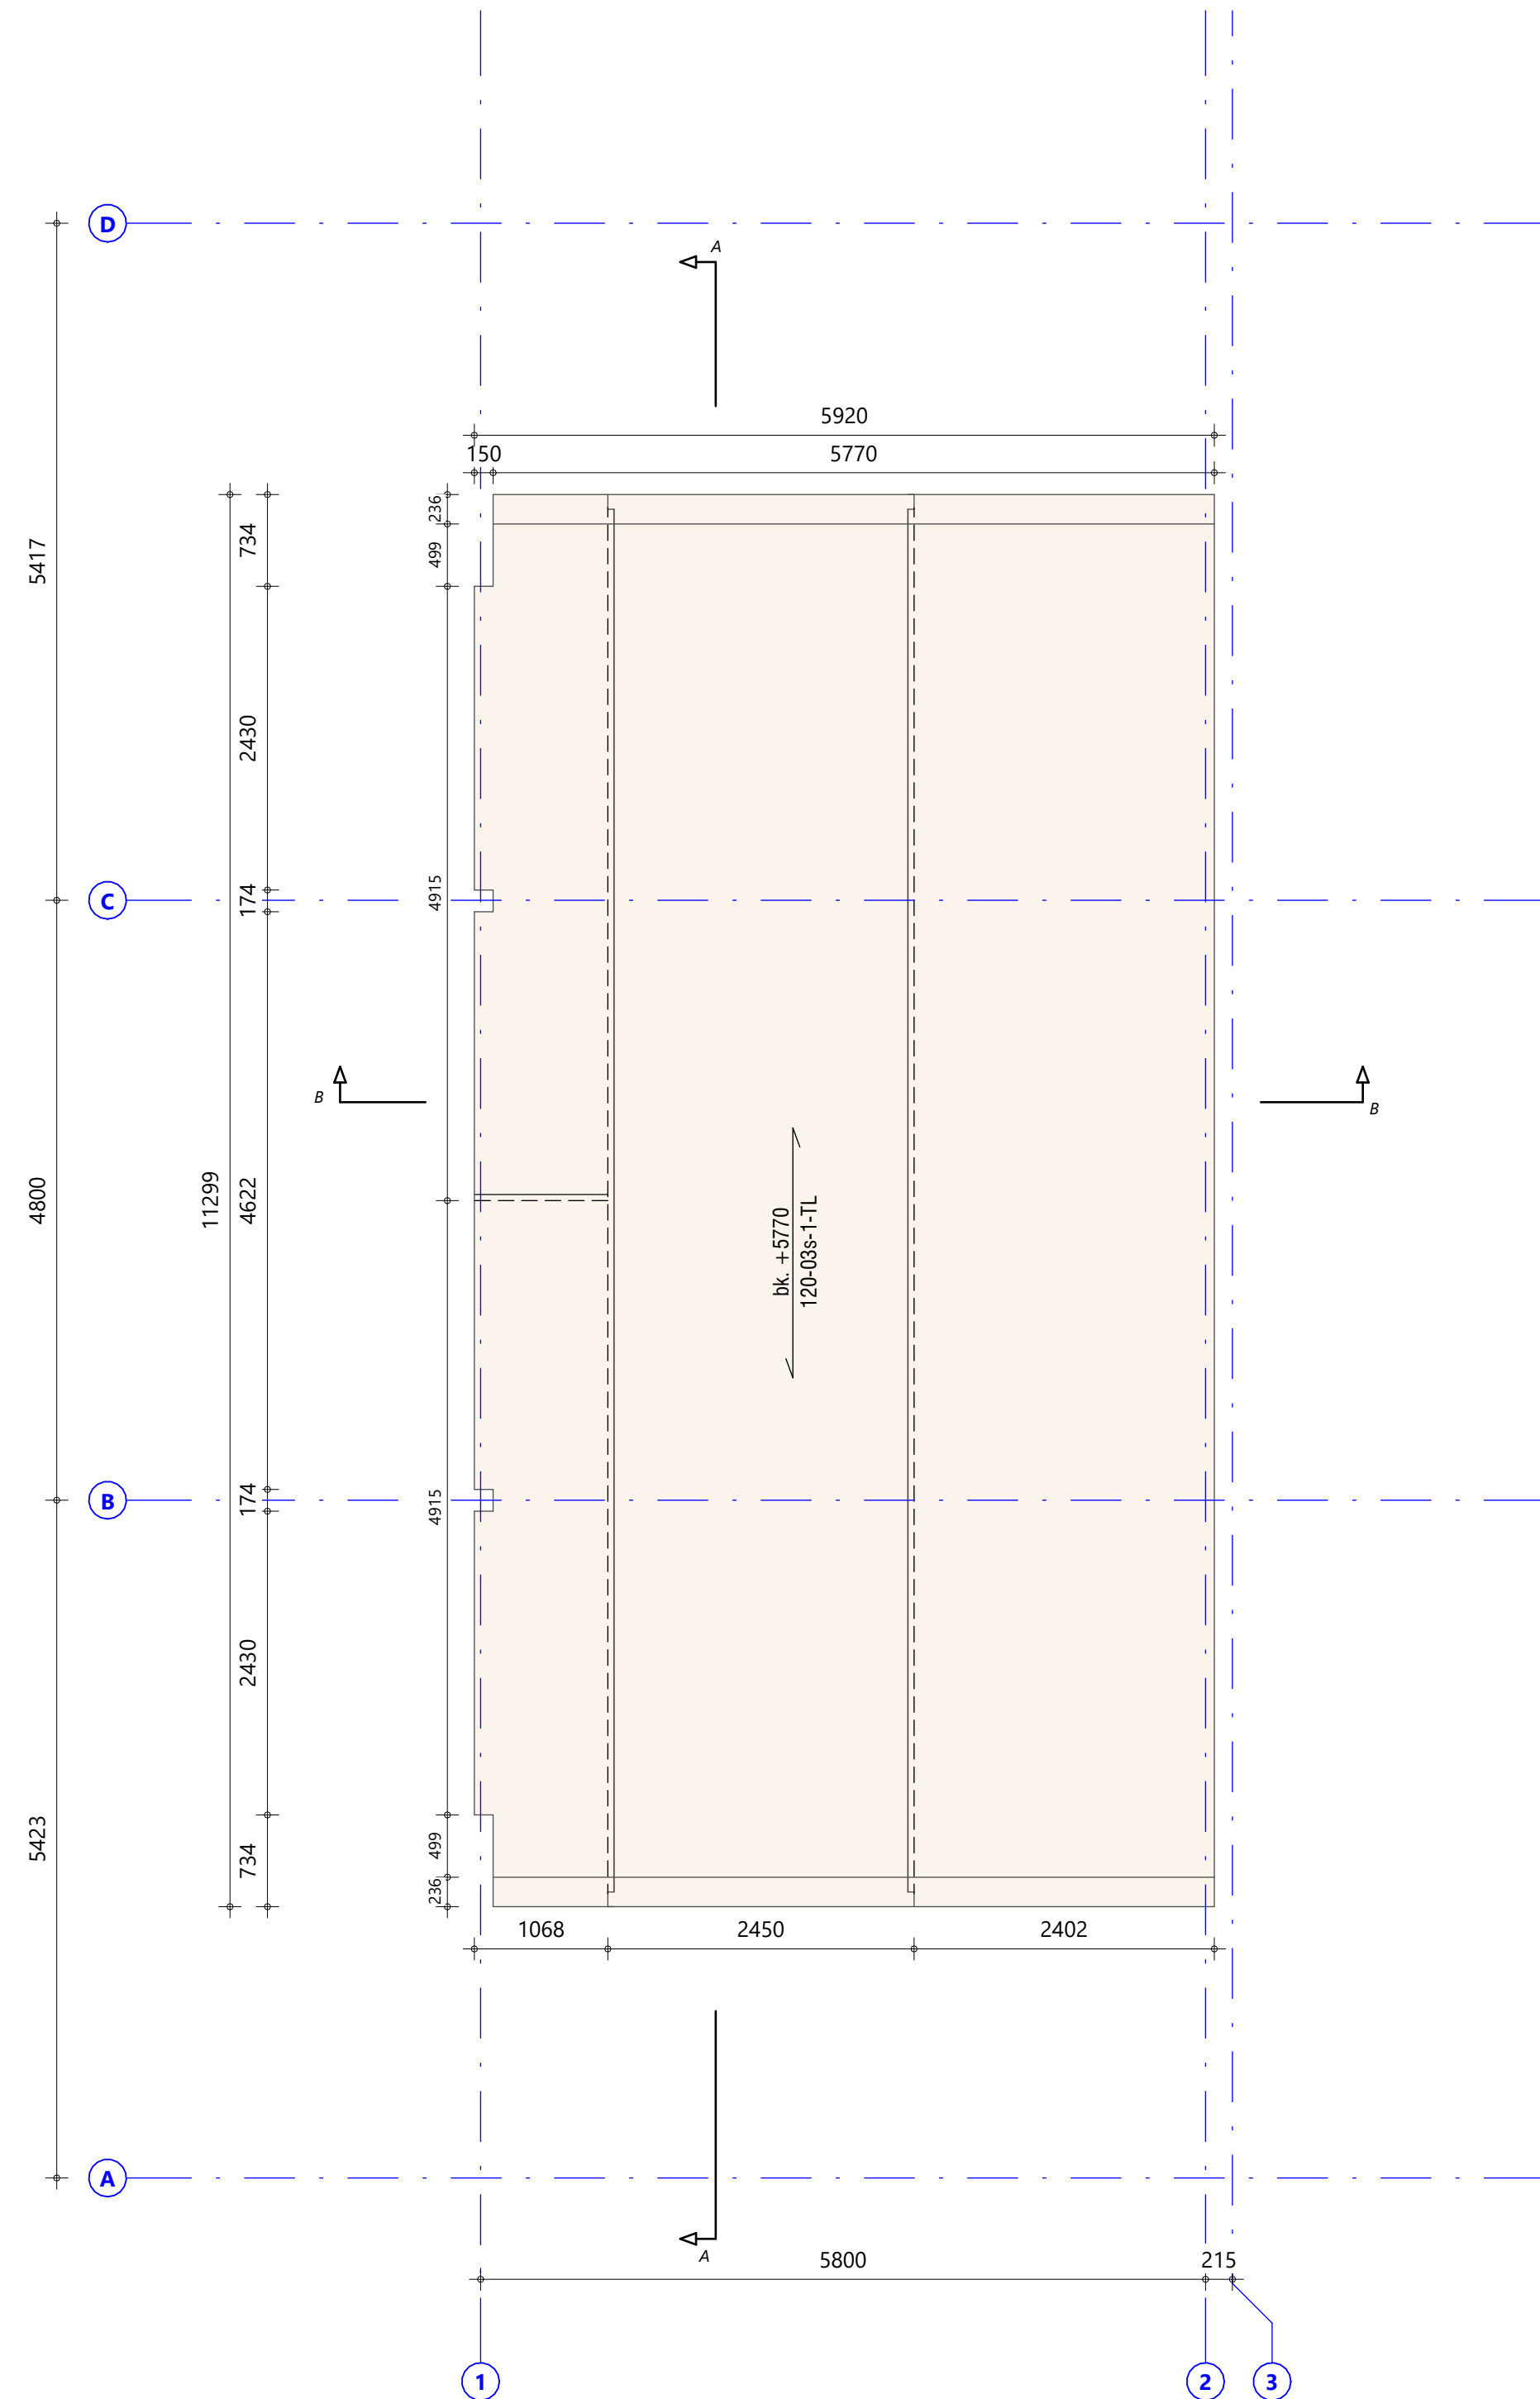

Sophialaan 7a
3542 AR Utrecht
T: +31 (0) 73 644 7500
E: info@jmconcepten.nl

Plattegrond 2e Verdieping

Vloeren Texel
Krimweg 53, de Cocksdorp

Opdrachtgever:

Projectnr: 3131
Fase:
Auteur: PMol

Formaat: A2
Schaal:
1^e datum: 04-05-2026
Status:
Tekeningnr: CLTP-03

Tekening ongeschikt voor uitvoeringsfase
Geprint 4-5-2026 14:58:57