


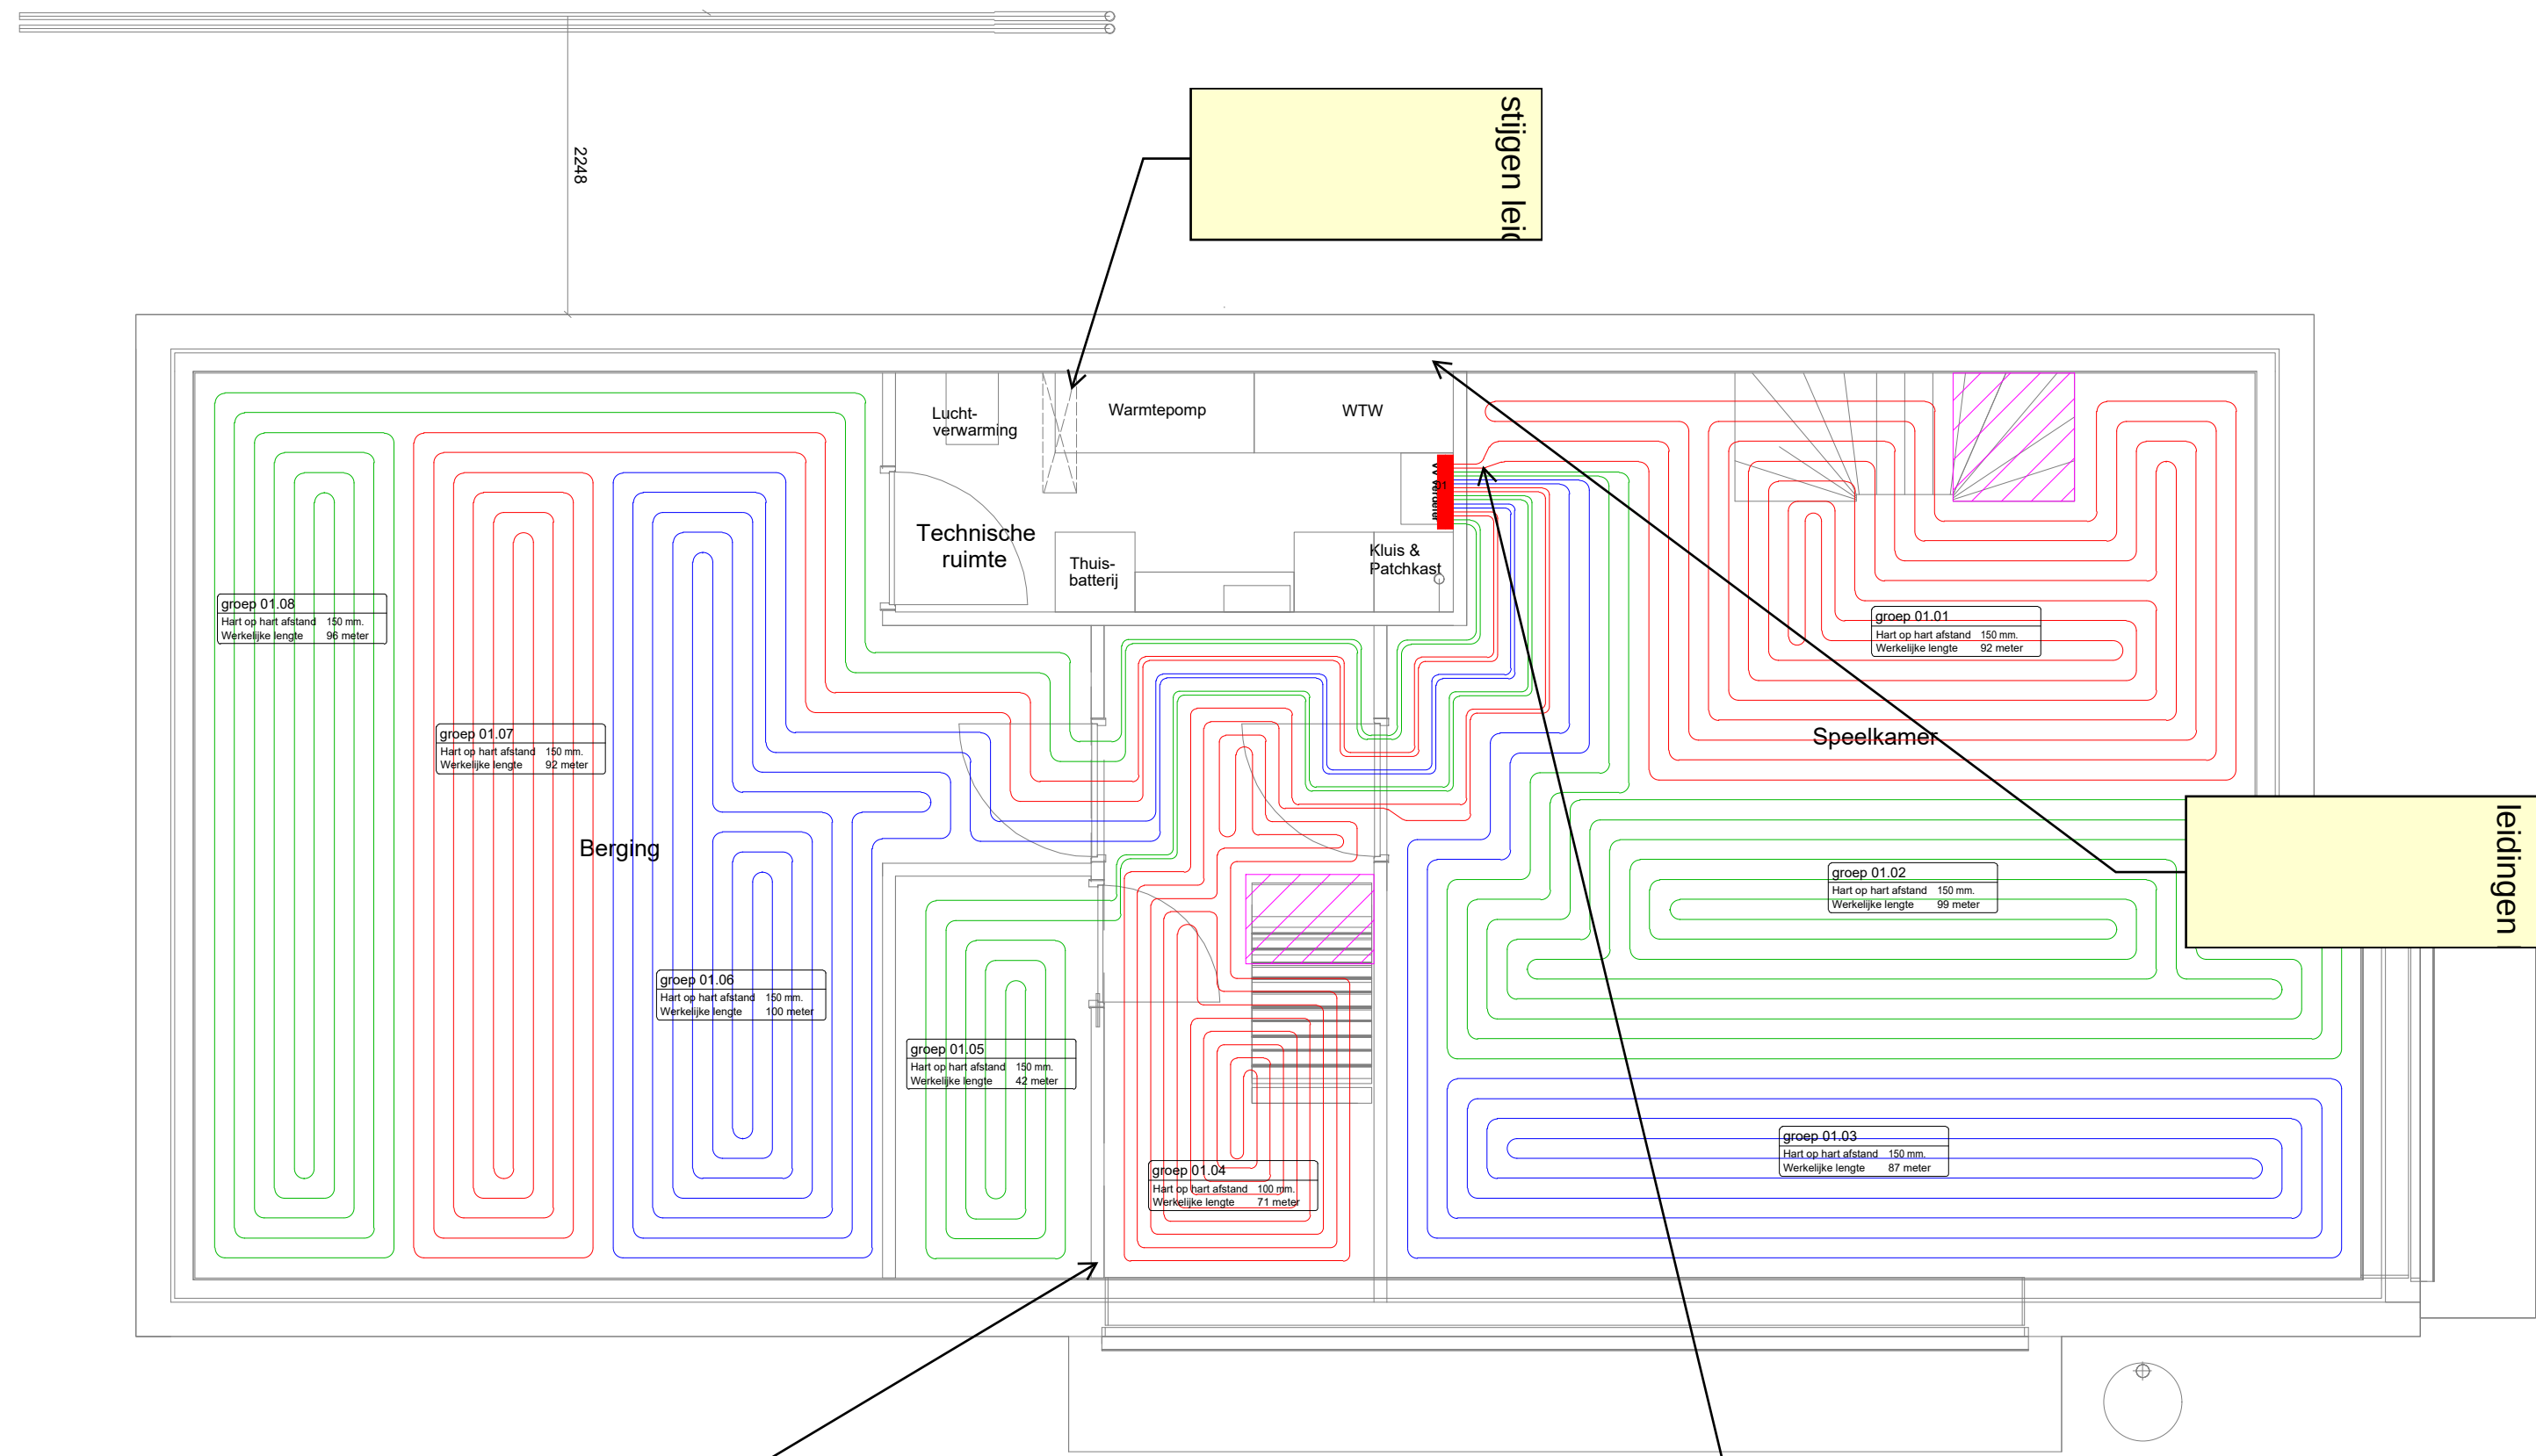


| Regelunit 01                               |                          |                                  |                   |             | Kunststof 8     |  |
|--------------------------------------------|--------------------------|----------------------------------|-------------------|-------------|-----------------|--|
| Leidingtype : PE-RT 16/2 mm                |                          | Primair drukverlies : 16.89 kPa. |                   |             |                 |  |
| Afmetingen in mm : h = 400 b = 555 d = 145 |                          | Secundair drukverlies : 0 kPa.   |                   |             |                 |  |
| Bevestigingsmateriaal: Vlechten            |                          | Temperatuur traject : 30/30°C    |                   |             |                 |  |
| Gr.                                        | Ruimte naam/Ruimtenummer | Ruimtetemperatuur(°C)            | Transmissie(Watt) | Debiet(l/m) | Vloerafwerking  |  |
| 01                                         | Berging                  | 18                               | 558               | 1.85        | Tapijt / parket |  |
| 02                                         | Berging                  | 18                               | 600               | 1.98        | Tapijt / parket |  |
| 03                                         | Berging                  | 18                               | 527               | 1.75        | Tapijt / parket |  |
| 04                                         | Gang                     | 18                               | 284               | 0.93        | Tapijt / parket |  |
| 05                                         | Ontberooide Ruimte       | 18                               | 255               | 0.83        | Tapijt / parket |  |
| 06                                         | Speelkamer               | 20                               | 606               | 2           | Tapijt / parket |  |
| 07                                         | Speelkamer               | 20                               | 558               | 1.85        | Tapijt / parket |  |
| 08                                         | Speelkamer               | 20                               | 582               | 1.92        | Tapijt / parket |  |

| Overzicht Groepen |         |           |
|-------------------|---------|-----------|
| Groepsnummer      | H.O.H.  | Lengte    |
| groep 01.01       | 150 mm. | 92 meter  |
| groep 01.02       | 150 mm. | 99 meter  |
| groep 01.03       | 150 mm. | 87 meter  |
| groep 01.04       | 100 mm. | 71 meter  |
| groep 01.05       | 150 mm. | 42 meter  |
| groep 01.06       | 150 mm. | 100 meter |
| groep 01.07       | 150 mm. | 92 meter  |
| groep 01.08       | 150 mm. | 96 meter  |
| Verdeler 01       | Totaal: | 679 meter |

Kelder

| Voorverwarmingsbus:                    |                        | PE-RT 20x2 mm: -               |                        | PE-RT 18x2 mm: - |                        | PE-RT 16x2 mm: 679 meter |                        | PE-RT 14x2 mm: - |                        |
|----------------------------------------|------------------------|--------------------------------|------------------------|------------------|------------------------|--------------------------|------------------------|------------------|------------------------|
| Nr. Type:                              | Bevestigingsmateriaal: | Nr. Type:                      | Bevestigingsmateriaal: | Nr. Type:        | Bevestigingsmateriaal: | Nr. Type:                | Bevestigingsmateriaal: | Nr. Type:        | Bevestigingsmateriaal: |
| 1                                      | Kunststof 8            | 8                              |                        | 15               |                        | 22                       |                        |                  |                        |
| 2                                      |                        | 9                              |                        | 16               |                        | 23                       |                        |                  |                        |
| 3                                      |                        | 10                             |                        | 17               |                        | 24                       |                        |                  |                        |
| 4                                      |                        | 11                             |                        | 18               |                        | 25                       |                        |                  |                        |
| 5                                      |                        | 12                             |                        | 19               |                        | 26                       |                        |                  |                        |
| 6                                      |                        | 13                             |                        | 20               |                        | 27                       |                        |                  |                        |
| 7                                      |                        | 14                             |                        | 21               |                        | 28                       |                        |                  |                        |
| Wijz. Datum:                           | Tekenaar:              | Omschrijving van de wijziging: |                        |                  |                        |                          |                        |                  |                        |
| 1                                      |                        |                                |                        |                  |                        |                          |                        |                  |                        |
| 2                                      |                        |                                |                        |                  |                        |                          |                        |                  |                        |
| 3                                      |                        |                                |                        |                  |                        |                          |                        |                  |                        |
| 4                                      |                        |                                |                        |                  |                        |                          |                        |                  |                        |
| 5                                      |                        |                                |                        |                  |                        |                          |                        |                  |                        |
| 6                                      |                        |                                |                        |                  |                        |                          |                        |                  |                        |
| 7                                      |                        |                                |                        |                  |                        |                          |                        |                  |                        |
| 8                                      |                        |                                |                        |                  |                        |                          |                        |                  |                        |
| Project naam : Woning B. van Dorp      |                        |                                |                        |                  |                        | <b>Ter Goedkeuring</b>   |                        |                  |                        |
| Project adres : Kralingseweg 370       |                        |                                |                        |                  |                        |                          |                        |                  |                        |
| Project postcode/plaats :              |                        |                                |                        |                  |                        |                          |                        |                  |                        |
| Projectnummer klant :                  |                        |                                |                        |                  |                        |                          |                        |                  |                        |
| Tekenaar : GCH                         |                        | Formaat : A1                   |                        | Projectnummer :  |                        |                          |                        |                  |                        |
| Tekendatum : 23-03-2026                |                        | Bladnummer : W-01              |                        |                  |                        |                          |                        |                  |                        |
| Bouwkundige tekening : 1368-Kelder.pdf |                        | Verdieping : Kelder            |                        |                  |                        |                          |                        |                  |                        |
| Datum bouwkl. tekening :               |                        | Schaal : 1:50 Type :           |                        |                  |                        |                          |                        |                  |                        |
|                                        |                        | Bouwnummer(s) :                |                        |                  |                        |                          |                        |                  |                        |

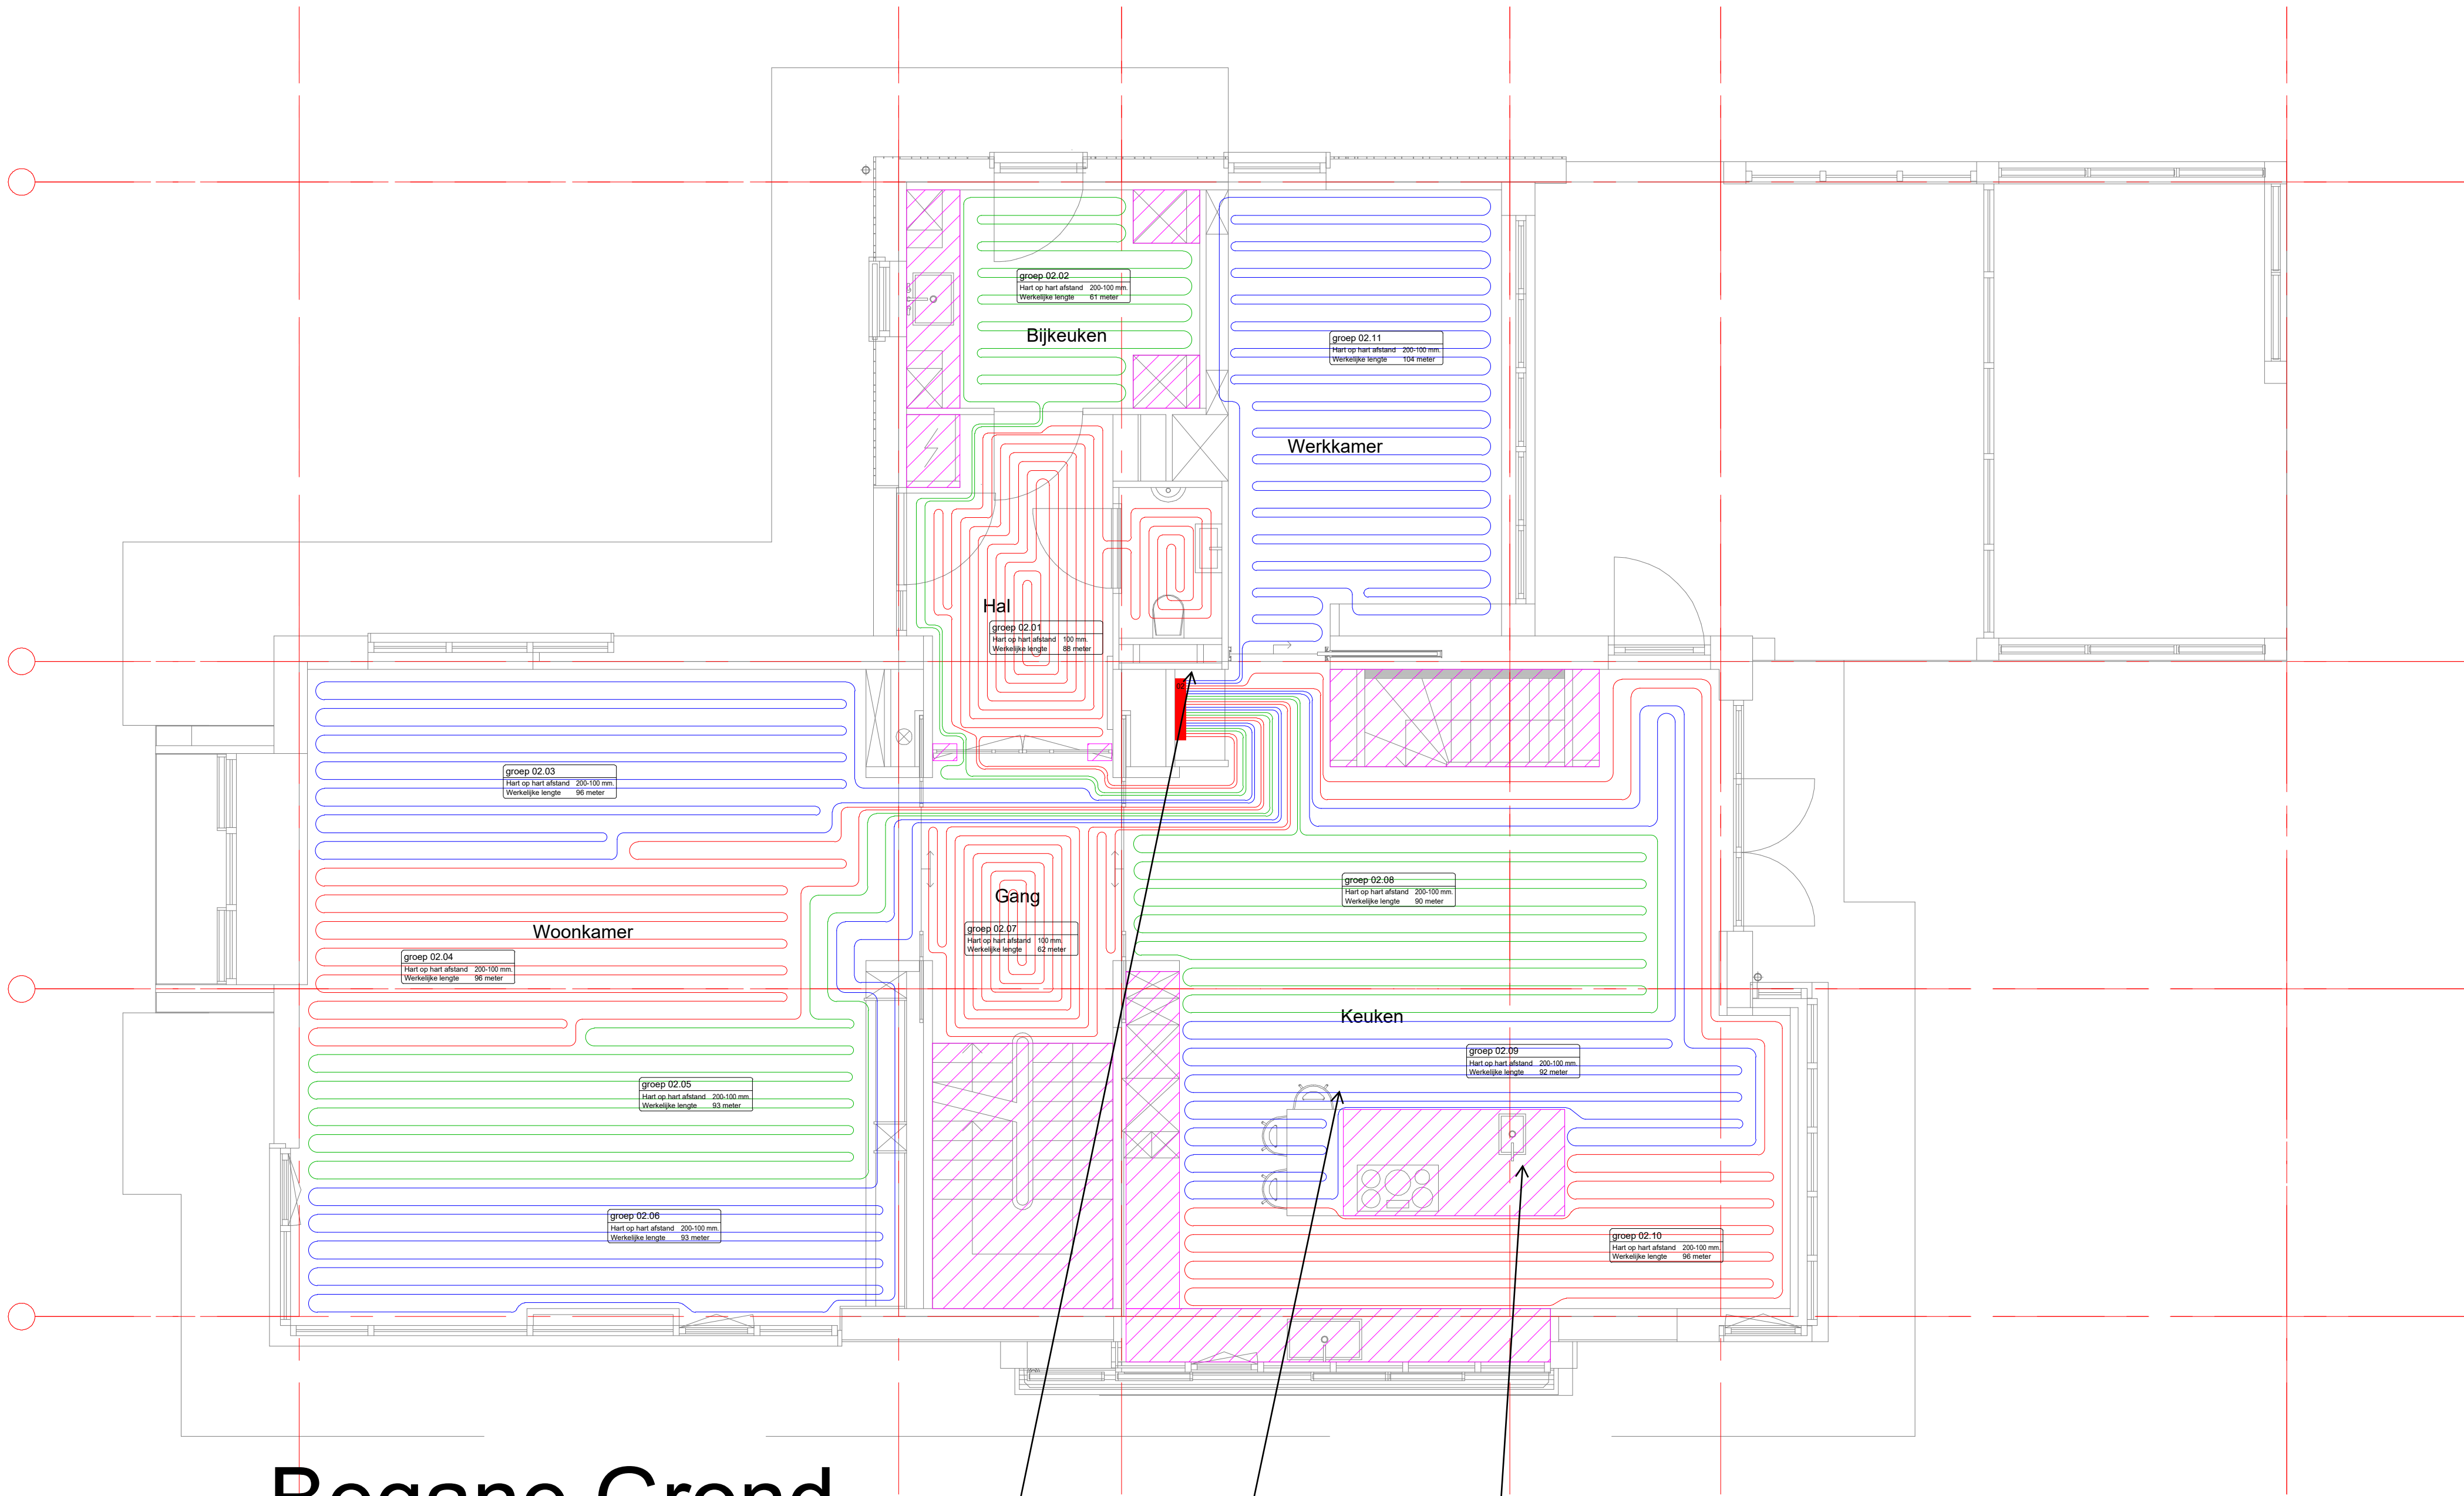


Begane Grond

| Regelunit 02                               |                         |                                  |                   | Kunststof 11 |                 |  |
|--------------------------------------------|-------------------------|----------------------------------|-------------------|--------------|-----------------|--|
| Leidingtype : PE-RT 18'2 mm                |                         | Primair drukverlies : 19.83 kPa. |                   |              |                 |  |
| Afmetingen in mm : h = 400 b = 600 d = 145 |                         | Secundair drukverlies : 0 kPa.   |                   |              |                 |  |
| Bevestigingsmateriaal : Tackeren/Vlechten  |                         | Temperatuur traject : 35/30°C    |                   |              |                 |  |
| Gr.                                        | Ruimtenaam/Ruimtenummer | Ruimtetemperatuur(°C)            | Transmissie(Watt) | Debiet(l/m)  | Vloerafwerking  |  |
| 01                                         | hal                     | 18                               | 523               | 1.73         | Tapijt / parket |  |
| 02                                         | Bijkeuken               | 18                               | 471               | 1.55         | Tapijt / parket |  |
| 03                                         | Woonkamer               | 22                               | 533               | 1.77         | Tapijt / parket |  |
| 04                                         | Woonkamer               | 22                               | 535               | 1.77         | Tapijt / parket |  |
| 05                                         | Woonkamer               | 22                               | 530               | 1.75         | Tapijt / parket |  |
| 06                                         | Woonkamer               | 22                               | 530               | 1.75         | Tapijt / parket |  |
| 07                                         | Gang                    | 18                               | 369               | 1.22         | Tapijt / parket |  |
| 08                                         | Keuken                  | 22                               | 536               | 1.77         | Tapijt / parket |  |
| 09                                         | Keuken                  | 22                               | 538               | 1.78         | Tapijt / parket |  |
| 10                                         | Keuken                  | 22                               | 540               | 1.78         | Tapijt / parket |  |
| 11                                         | Werkkamer               | 22                               | 550               | 1.82         | Tapijt / parket |  |

| Overzicht Groepen |             |           |
|-------------------|-------------|-----------|
| Groepsnummer      | H.O.H.      | Lengte    |
| groep 02.01       | 100 mm.     | 88 meter  |
| groep 02.02       | 200-100 mm. | 61 meter  |
| groep 02.03       | 200-100 mm. | 96 meter  |
| groep 02.04       | 200-100 mm. | 96 meter  |
| groep 02.05       | 200-100 mm. | 93 meter  |
| groep 02.06       | 200-100 mm. | 93 meter  |
| groep 02.07       | 100 mm.     | 62 meter  |
| groep 02.08       | 200-100 mm. | 90 meter  |
| groep 02.09       | 200-100 mm. | 92 meter  |
| groep 02.10       | 200-100 mm. | 96 meter  |
| groep 02.11       | 200-100 mm. | 104 meter |
| Verdeler 02       | Totaal:     | 971 meter |

| Vloerverwarmingsbuis    |              | PE-RT 20x2 mm. -       |                                              | PE-RT 18x2 mm. - |                        | PE-RT 16x2 mm. 971 meter |       | PE-RT 14x2 mm. -       |                           |       |                        |
|-------------------------|--------------|------------------------|----------------------------------------------|------------------|------------------------|--------------------------|-------|------------------------|---------------------------|-------|------------------------|
| Nr.                     | Type:        | Bevestigingsmateriaal: | Nr.                                          | Type:            | Bevestigingsmateriaal: | Nr.                      | Type: | Bevestigingsmateriaal: | Nr.                       | Type: | Bevestigingsmateriaal: |
| 1                       | Kunststof 11 | Tackeren/Vlechten      | 8                                            |                  |                        | 15                       |       |                        | 22                        |       |                        |
| 2                       |              |                        | 9                                            |                  |                        | 16                       |       |                        | 23                        |       |                        |
| 3                       |              |                        | 10                                           |                  |                        | 17                       |       |                        | 24                        |       |                        |
| 4                       |              |                        | 11                                           |                  |                        | 18                       |       |                        | 25                        |       |                        |
| 5                       |              |                        | 12                                           |                  |                        | 19                       |       |                        | 26                        |       |                        |
| 6                       |              |                        | 13                                           |                  |                        | 20                       |       |                        | 27                        |       |                        |
| 7                       |              |                        | 14                                           |                  |                        | 21                       |       |                        | 28                        |       |                        |
| Wijz.                   | Datum:       | Tekenaar:              | Omschrijving van de wijziging:               |                  |                        |                          |       |                        |                           |       |                        |
| 1                       |              |                        |                                              |                  |                        |                          |       |                        |                           |       |                        |
| 2                       |              |                        |                                              |                  |                        |                          |       |                        |                           |       |                        |
| 3                       |              |                        |                                              |                  |                        |                          |       |                        |                           |       |                        |
| 4                       |              |                        |                                              |                  |                        |                          |       |                        |                           |       |                        |
| 5                       |              |                        |                                              |                  |                        |                          |       |                        |                           |       |                        |
| 6                       |              |                        |                                              |                  |                        |                          |       |                        |                           |       |                        |
| 7                       |              |                        |                                              |                  |                        |                          |       |                        |                           |       |                        |
| 8                       |              |                        |                                              |                  |                        |                          |       |                        |                           |       |                        |
| Project naam            |              |                        | : Woning B. van Dorp                         |                  |                        |                          |       |                        |                           |       |                        |
| Project adres           |              |                        | : Kralingseweg 370                           |                  |                        |                          |       |                        |                           |       |                        |
| Project postcode/plaats |              |                        |                                              |                  |                        |                          |       |                        |                           |       |                        |
| Projectnummer klant     |              |                        |                                              |                  |                        |                          |       |                        |                           |       |                        |
| Tekenaar                |              |                        | : GCH                                        |                  |                        | Formaat : A1             |       |                        | <b>Ter Goedkeuring</b>    |       |                        |
| Tekendatum              |              |                        | : 23-03-2026                                 |                  |                        |                          |       |                        | Projectnummer :           |       |                        |
| Bouwkundige tekening    |              |                        | : 2025-05-29_Kralingseweg 370_Update Beg.Gr. |                  |                        |                          |       |                        | Bladnummer : W00          |       |                        |
| Datum bouwkl. tekening  |              |                        |                                              |                  |                        |                          |       |                        | Verdieping : Begane grond |       |                        |
|                         |              |                        |                                              |                  |                        |                          |       |                        | Schaal : 1:50 Type :      |       |                        |
|                         |              |                        |                                              |                  |                        |                          |       |                        | Gebouw :                  |       |                        |
|                         |              |                        |                                              |                  |                        |                          |       |                        | Bouwnummer(s) :           |       |                        |



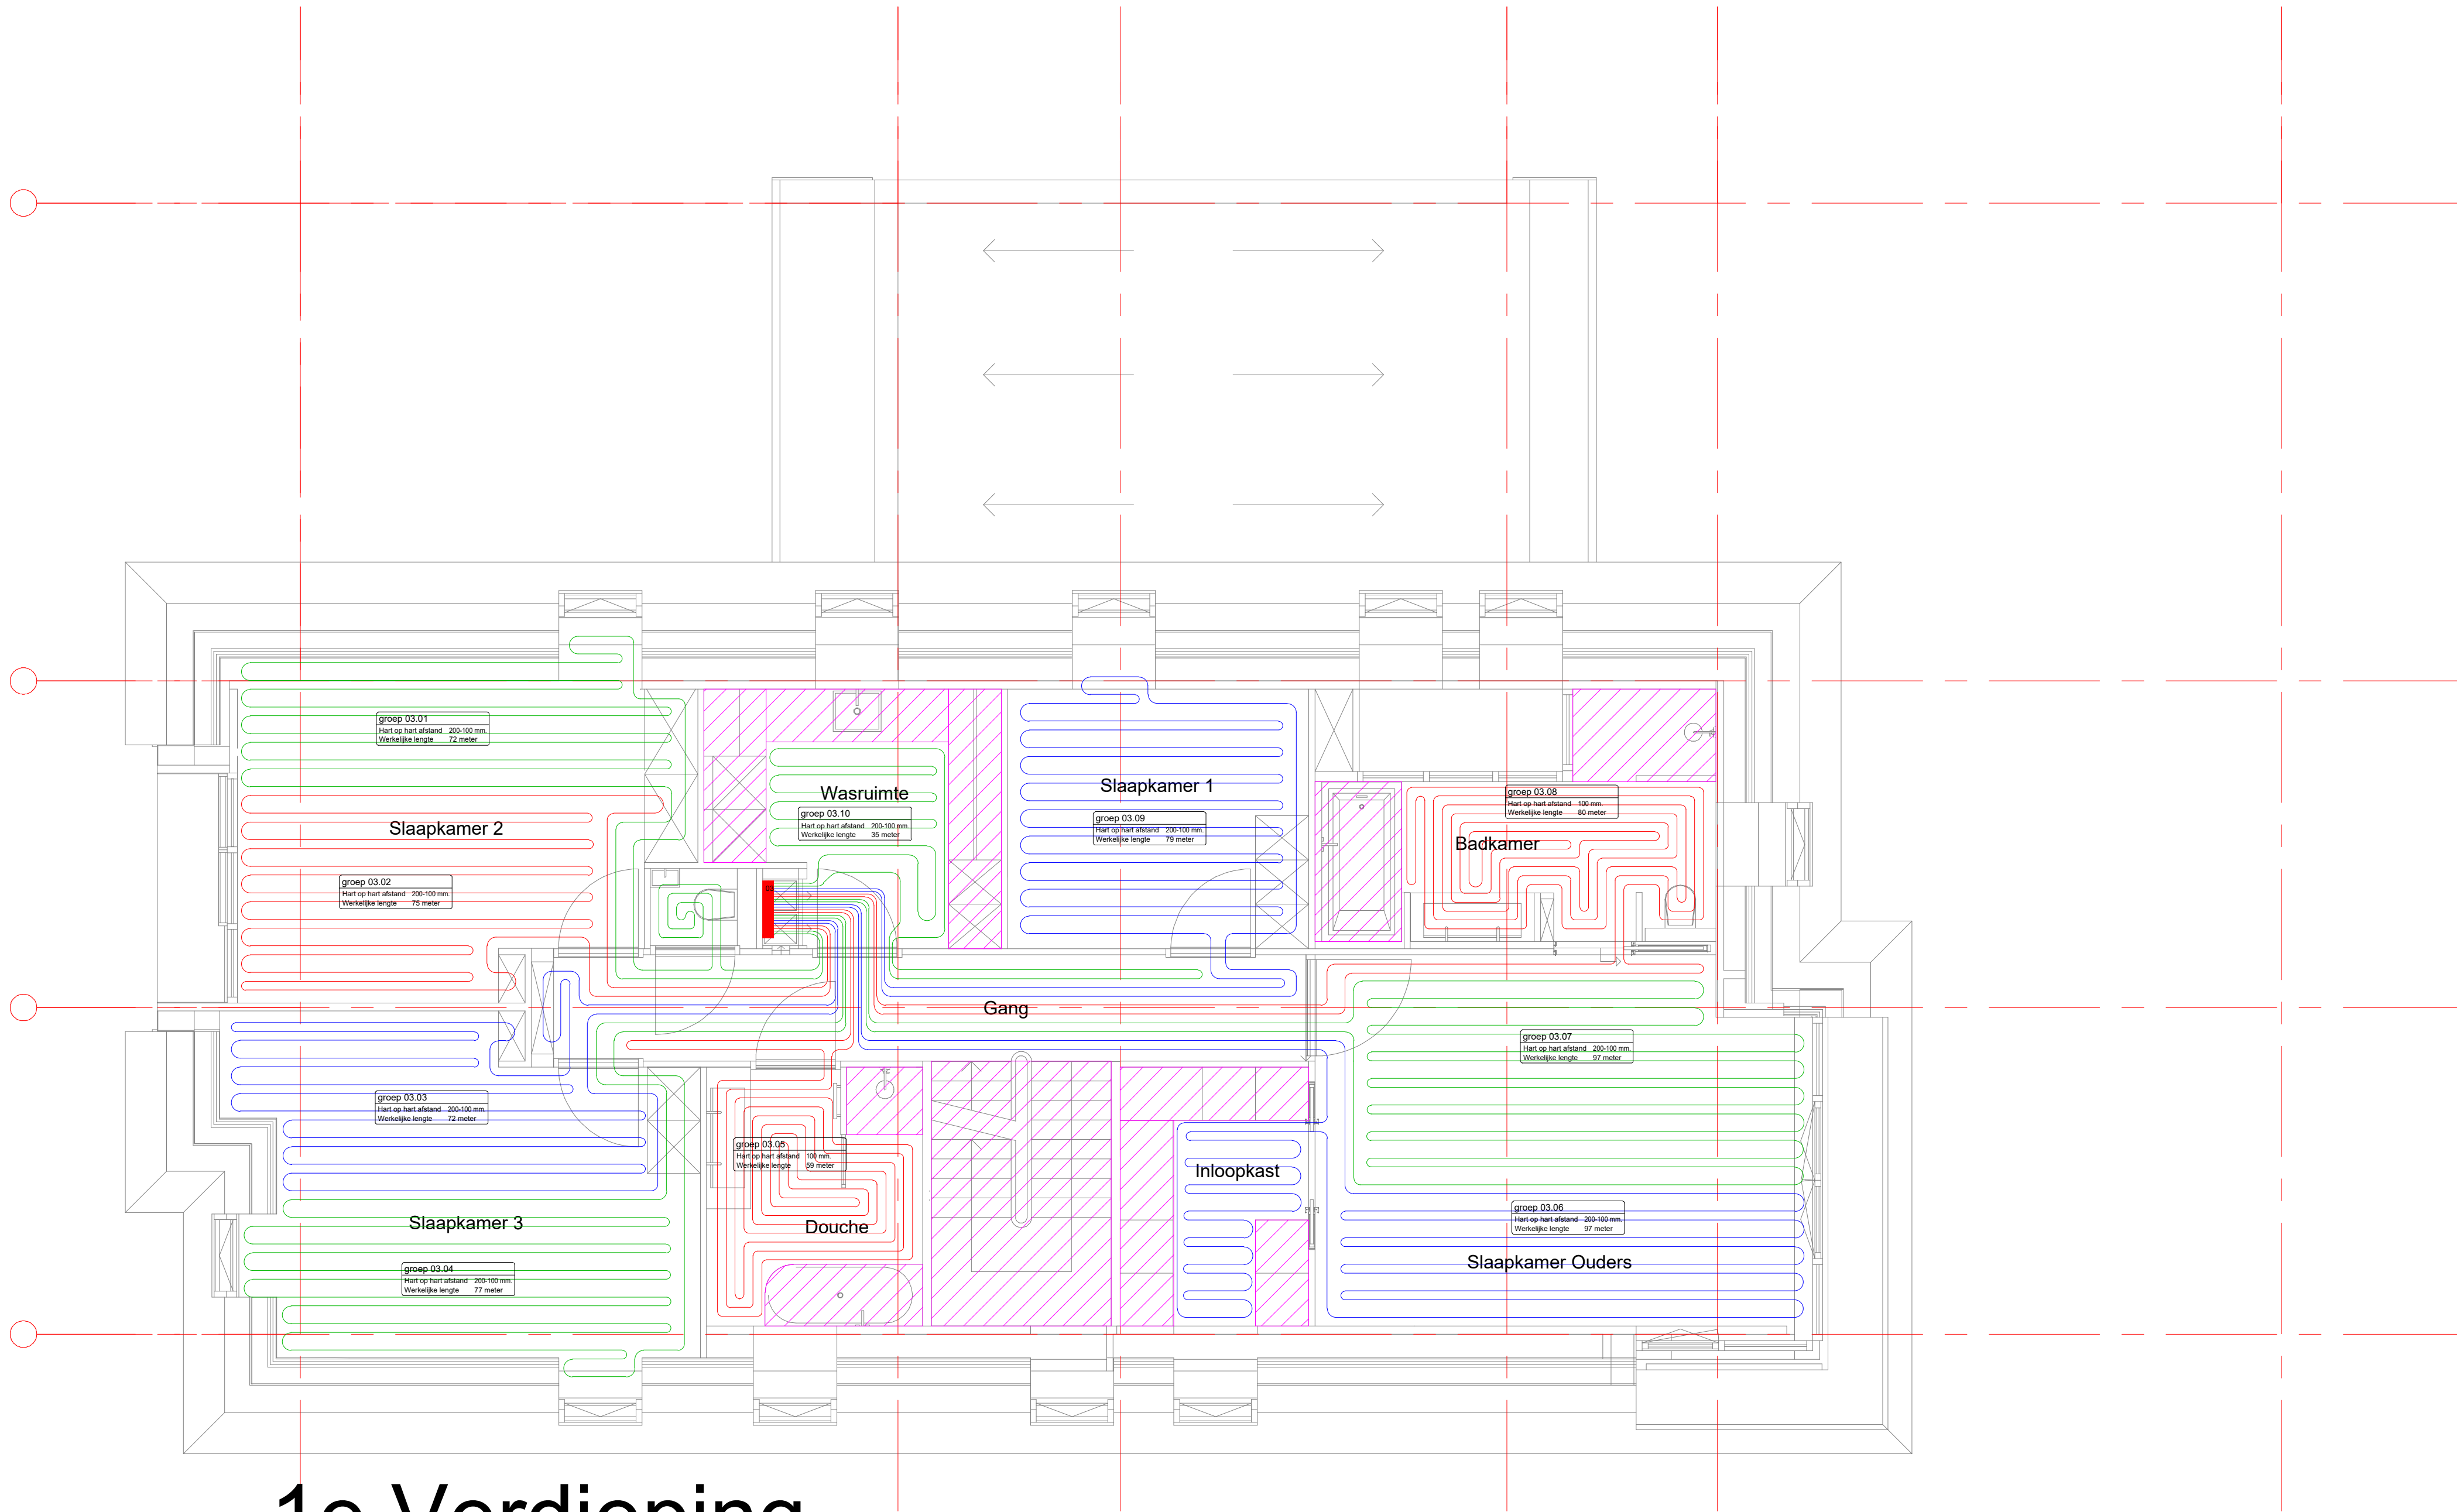


1e Verdieping

| Regelunit 03                               |                         |                                 |                   |             | Kunststof 10    |  |  |  |
|--------------------------------------------|-------------------------|---------------------------------|-------------------|-------------|-----------------|--|--|--|
| Leidingtype : PE-RT 16/2 mm                |                         | Primair drukverlies : 18,32 kPa |                   |             |                 |  |  |  |
| Afmetingen in mm : h = 400 b = 645 d = 145 |                         | Secundair drukverlies : 0 kPa   |                   |             |                 |  |  |  |
| Bevestigingsmateriaal : Tackeren/Vlechten  |                         | Temperatuur traject : 35/30°C   |                   |             |                 |  |  |  |
| Gr.                                        | Ruimtenaam/Ruimtenummer | Ruimtetemperatuur(°C)           | Transmissie(Watt) | Debiet(l/m) | Vloerafwerking  |  |  |  |
| 01                                         | Slaapkamer 2            | 22                              | 465               | 1.53        | Tap(t) / parket |  |  |  |
| 02                                         | Slaapkamer 2            | 22                              | 484               | 1.6         | Tap(t) / parket |  |  |  |
| 03                                         | Slaapkamer 3            | 22                              | 465               | 1.53        | Tap(t) / parket |  |  |  |
| 04                                         | Slaapkamer 3            | 22                              | 497               | 1.65        | Tap(t) / parket |  |  |  |
| 05                                         | Douche                  | 22                              | 434               | 1.43        | Steen / PVC     |  |  |  |
| 06                                         | Slaapkamer Ouders       | 22                              | 592               | 1.95        | Tap(t) / parket |  |  |  |
| 07                                         | Slaapkamer Ouders       | 22                              | 593               | 1.97        | Tap(t) / parket |  |  |  |
| 08                                         | Badkamer                | 22                              | 589               | 1.95        | Steen / PVC     |  |  |  |
| 09                                         | Slaapkamer 1            | 22                              | 510               | 1.68        | Tap(t) / parket |  |  |  |
| 10                                         | Wasseruite              | 20                              | 247               | 0.82        | Tap(t) / parket |  |  |  |

| Overzicht Groepen |             |           |
|-------------------|-------------|-----------|
| Groepsnummer      | H.O.H.      | Lengte    |
| groep 03.01       | 200-100 mm. | 72 meter  |
| groep 03.02       | 200-100 mm. | 75 meter  |
| groep 03.03       | 200-100 mm. | 72 meter  |
| groep 03.04       | 200-100 mm. | 77 meter  |
| groep 03.05       | 100 mm.     | 59 meter  |
| groep 03.06       | 200-100 mm. | 97 meter  |
| groep 03.07       | 200-100 mm. | 97 meter  |
| groep 03.08       | 100 mm.     | 80 meter  |
| groep 03.09       | 200-100 mm. | 79 meter  |
| groep 03.10       | 200-100 mm. | 35 meter  |
| Verdeler 03       | Totaal:     | 743 meter |

| Vloerverwarmingsbuis    |              | PE-RT 20x2 mm. -                              | PE-RT 18x2 mm. - | PE-RT 16x2 mm. 743 meter       | PE-RT 14x2 mm. -       |                            |       |
|-------------------------|--------------|-----------------------------------------------|------------------|--------------------------------|------------------------|----------------------------|-------|
| Nr.                     | Type:        | Bevestigingsmateriaal:                        | Nr.              | Type:                          | Bevestigingsmateriaal: | Nr.                        | Type: |
| 1                       |              | 8                                             |                  | 15                             |                        | 22                         |       |
| 2                       |              | 9                                             |                  | 16                             |                        | 23                         |       |
| 3                       | Kunststof 10 | Tackeren/Vlechten                             | 10               |                                |                        | 24                         |       |
| 4                       |              | 11                                            |                  | 18                             |                        | 25                         |       |
| 5                       |              | 12                                            |                  | 19                             |                        | 26                         |       |
| 6                       |              | 13                                            |                  | 20                             |                        | 27                         |       |
| 7                       |              | 14                                            |                  | 21                             |                        | 28                         |       |
| Wijz. Datum:            |              | Tekenaar:                                     |                  | Omschrijving van de wijziging: |                        |                            |       |
| 1                       |              |                                               |                  |                                |                        |                            |       |
| 2                       |              |                                               |                  |                                |                        |                            |       |
| 3                       |              |                                               |                  |                                |                        |                            |       |
| 4                       |              |                                               |                  |                                |                        |                            |       |
| 5                       |              |                                               |                  |                                |                        |                            |       |
| 6                       |              |                                               |                  |                                |                        |                            |       |
| 7                       |              |                                               |                  |                                |                        |                            |       |
| 8                       |              |                                               |                  |                                |                        |                            |       |
| Project naam            |              | : Woning B. van Dorp                          |                  |                                |                        | <b>Ter Goedkeuring</b>     |       |
| Project adres           |              | : Kralingseweg 370                            |                  |                                |                        |                            |       |
| Project postcode/plaats |              | :                                             |                  |                                |                        |                            |       |
| Projectnummer klant     |              | :                                             |                  |                                |                        |                            |       |
| Tekenaar                |              | : GCH                                         |                  | Formaat : A1                   |                        | Projectnummer :            |       |
| Tekendatum              |              | : 23-03-2026                                  |                  |                                |                        | Bladnummer : W01           |       |
| Bouwkundige tekening    |              | : 2025-05-29_Kralingseweg 370_Update 1e Verd. |                  |                                |                        | Verdieping : 1e Verdieping |       |
| Datum bouw. tekening    |              | :                                             |                  |                                |                        | Schaal : 1:50 Type :       |       |
|                         |              |                                               |                  |                                |                        | Gebouw :                   |       |
|                         |              |                                               |                  |                                |                        | Bouwnummer(s) :            |       |

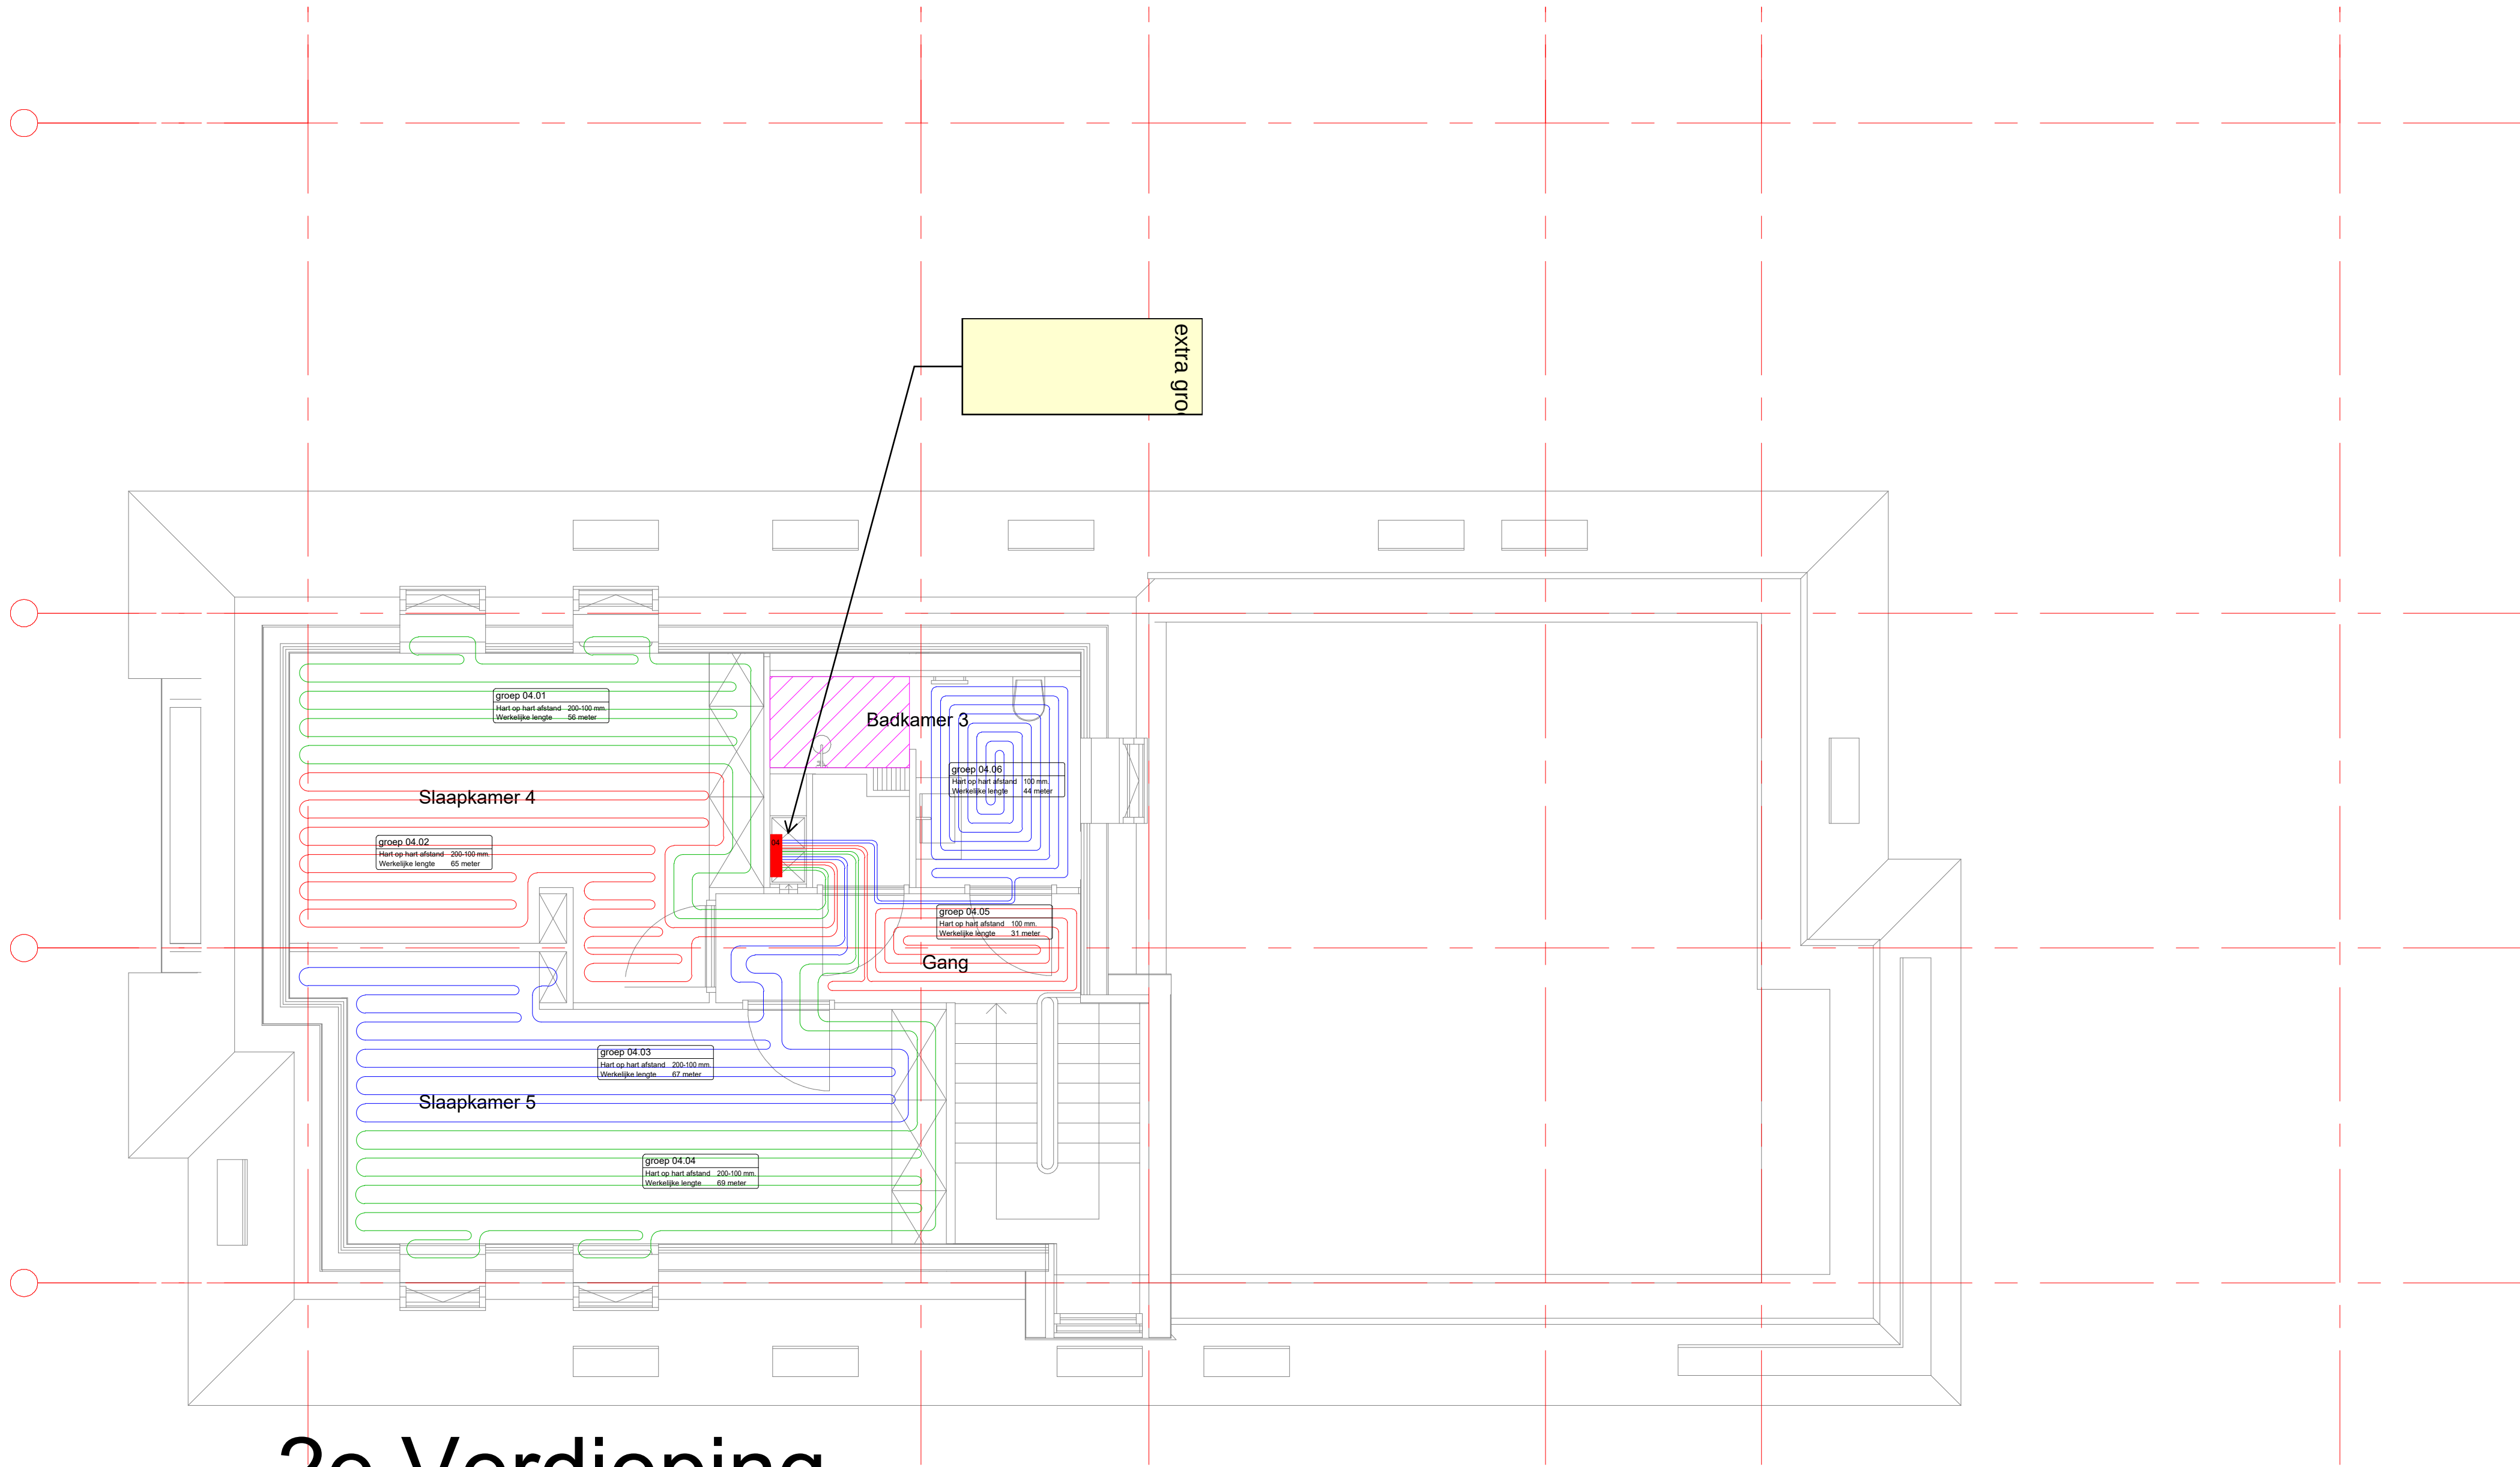

2e Verdieping

| Regelunit 04                               |                         |                                |                   | Kunststof 6 |                |  |  |
|--------------------------------------------|-------------------------|--------------------------------|-------------------|-------------|----------------|--|--|
| Leidingtype : PE-RT 16x2 mm                |                         | Primair drukverlies : 5.58 kPa |                   |             |                |  |  |
| Afmetingen in mm : h = 400 b = 465 d = 145 |                         | Secundair drukverlies : 0 kPa  |                   |             |                |  |  |
| Bevestigingsmateriaal: Tackeren/Vechten    |                         | Temperatuur traject : 35/30°C  |                   |             |                |  |  |
| Gr                                         | Ruimtenaam/Ruimtenummer | Ruimtetemperatuur(°C)          | Transmissie(Watt) | Debiet(l/m) | Vloerafwerking |  |  |
| 01                                         | Slaapkamer 4            | 22                             | 362               | 1.2         | Tap@ / parket  |  |  |
| 02                                         | Slaapkamer 4            | 22                             | 420               | 1.38        | Tap@ / parket  |  |  |
| 03                                         | Slaapkamer 5            | 22                             | 435               | 1.43        | Tap@ / parket  |  |  |
| 04                                         | Slaapkamer 5            | 22                             | 446               | 1.47        | Tap@ / parket  |  |  |
| 05                                         | Gang                    | 18                             | 184               | 0.82        | Tap@ / parket  |  |  |
| 06                                         | Badkamer                | 22                             | 324               | 1.07        | Steen / PVC    |  |  |

| Overzicht Groepen |             |           |
|-------------------|-------------|-----------|
| Groepsnummer      | H.O.H.      | Lengte    |
| groep 04.01       | 200-100 mm. | 56 meter  |
| groep 04.02       | 200-100 mm. | 65 meter  |
| groep 04.03       | 200-100 mm. | 67 meter  |
| groep 04.04       | 200-100 mm. | 69 meter  |
| groep 04.05       | 100 mm.     | 31 meter  |
| groep 04.06       | 100 mm.     | 44 meter  |
| Verdelers 04      | Totaal:     | 332 meter |

| Vloerverwarmingsbus:    |             | PE-RT 20x2 mm: -       |  | PE-RT 18x2 mm: -               |       | PE-RT 16x2 mm: 332 meter                      |  | PE-RT 14x2 mm: - |       |                        |  |                            |  |  |  |
|-------------------------|-------------|------------------------|--|--------------------------------|-------|-----------------------------------------------|--|------------------|-------|------------------------|--|----------------------------|--|--|--|
| Nr.:                    | Type:       | Bevestigingsmateriaal: |  | Nr.:                           | Type: | Bevestigingsmateriaal:                        |  | Nr.:             | Type: | Bevestigingsmateriaal: |  |                            |  |  |  |
| 1                       |             | 8                      |  |                                |       | 15                                            |  |                  |       | 22                     |  |                            |  |  |  |
| 2                       |             | 9                      |  |                                |       | 16                                            |  |                  |       | 23                     |  |                            |  |  |  |
| 3                       |             | 10                     |  |                                |       | 17                                            |  |                  |       | 24                     |  |                            |  |  |  |
| 4                       | Kunststof 6 | Tackeren/Vechten       |  | 11                             |       | 18                                            |  |                  |       | 25                     |  |                            |  |  |  |
| 5                       |             | 12                     |  |                                |       | 19                                            |  |                  |       | 26                     |  |                            |  |  |  |
| 6                       |             | 13                     |  |                                |       | 20                                            |  |                  |       | 27                     |  |                            |  |  |  |
| 7                       |             | 14                     |  |                                |       | 21                                            |  |                  |       | 28                     |  |                            |  |  |  |
| Wijz. Datum:            |             | Tekenaar:              |  | Omschrijving van de wijziging: |       |                                               |  |                  |       |                        |  |                            |  |  |  |
| 1                       |             |                        |  |                                |       |                                               |  |                  |       |                        |  |                            |  |  |  |
| 2                       |             |                        |  |                                |       |                                               |  |                  |       |                        |  |                            |  |  |  |
| 3                       |             |                        |  |                                |       |                                               |  |                  |       |                        |  |                            |  |  |  |
| 4                       |             |                        |  |                                |       |                                               |  |                  |       |                        |  |                            |  |  |  |
| 5                       |             |                        |  |                                |       |                                               |  |                  |       |                        |  |                            |  |  |  |
| 6                       |             |                        |  |                                |       |                                               |  |                  |       |                        |  |                            |  |  |  |
| 7                       |             |                        |  |                                |       |                                               |  |                  |       |                        |  |                            |  |  |  |
| 8                       |             |                        |  |                                |       |                                               |  |                  |       |                        |  |                            |  |  |  |
| Project naam            |             |                        |  |                                |       | : Woning B. van Dorp                          |  |                  |       |                        |  |                            |  |  |  |
| Project adres           |             |                        |  |                                |       | : Kralingseweg 370                            |  |                  |       |                        |  |                            |  |  |  |
| Project postcode/plaats |             |                        |  |                                |       |                                               |  |                  |       |                        |  |                            |  |  |  |
| Projectnummer klant     |             |                        |  |                                |       |                                               |  |                  |       |                        |  |                            |  |  |  |
| Tekenaar                |             |                        |  |                                |       | : GCH                                         |  | Formaat : A1     |       | <b>Ter Goedkeuring</b> |  |                            |  |  |  |
| Tekendatum              |             |                        |  |                                |       | : 23-03-2026                                  |  |                  |       | Projectnummer :        |  |                            |  |  |  |
| Bouwkundige tekening    |             |                        |  |                                |       | : 2025-05-29_Kralingseweg 370_Update 2e Verd. |  |                  |       |                        |  | Bladnummer : W02           |  |  |  |
| Datum bouwkl. tekening  |             |                        |  |                                |       |                                               |  |                  |       |                        |  | Verdieping : 2e Verdieping |  |  |  |
|                         |             |                        |  |                                |       |                                               |  |                  |       |                        |  | Schaal : 1:50 Type :       |  |  |  |
|                         |             |                        |  |                                |       |                                               |  |                  |       |                        |  | Gebouw :                   |  |  |  |
|                         |             |                        |  |                                |       |                                               |  |                  |       |                        |  | Bouwnummer(s) :            |  |  |  |