



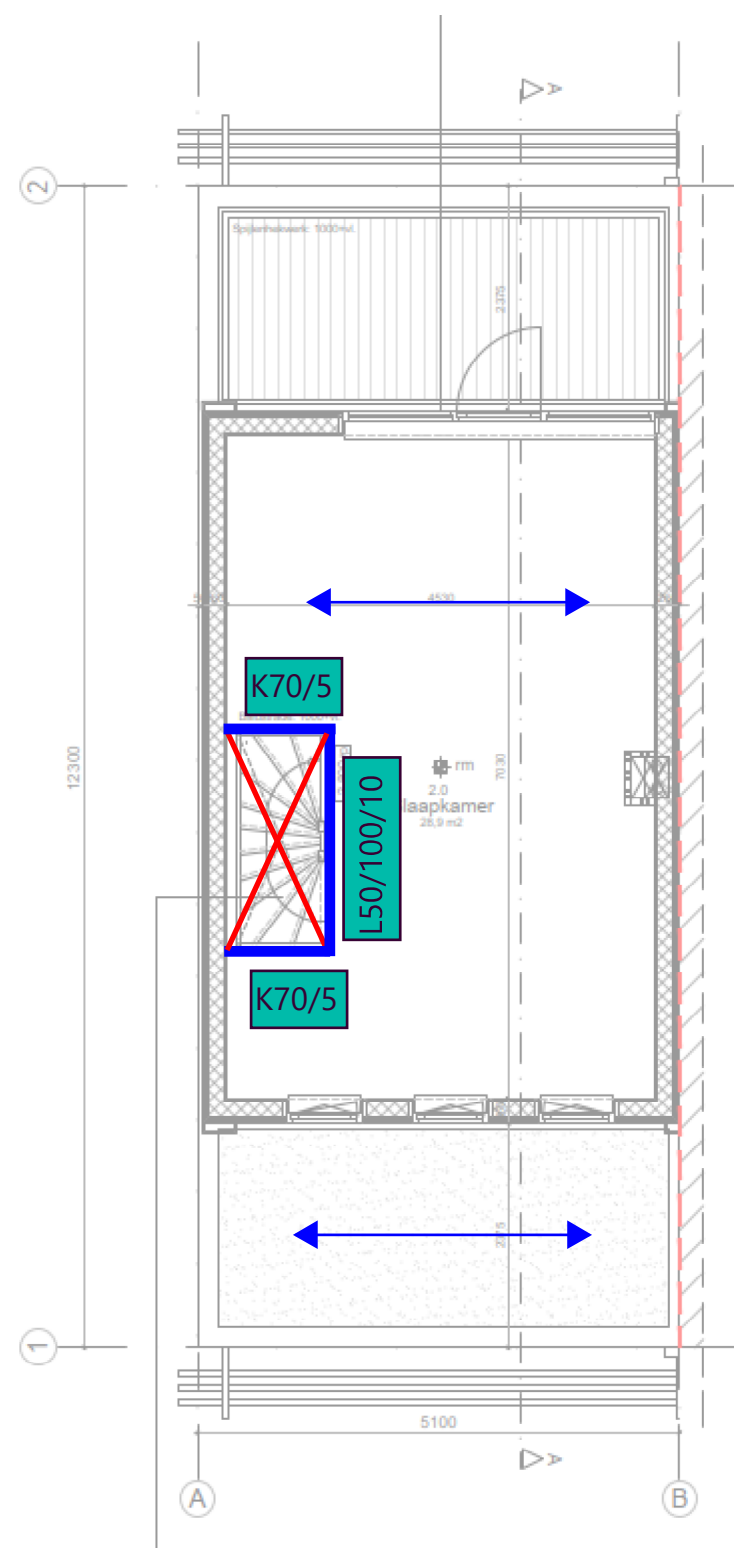

CONSTRUCTIE 2E VERDIEPING

- dragende wand
- ↔ bestaande betonvloer

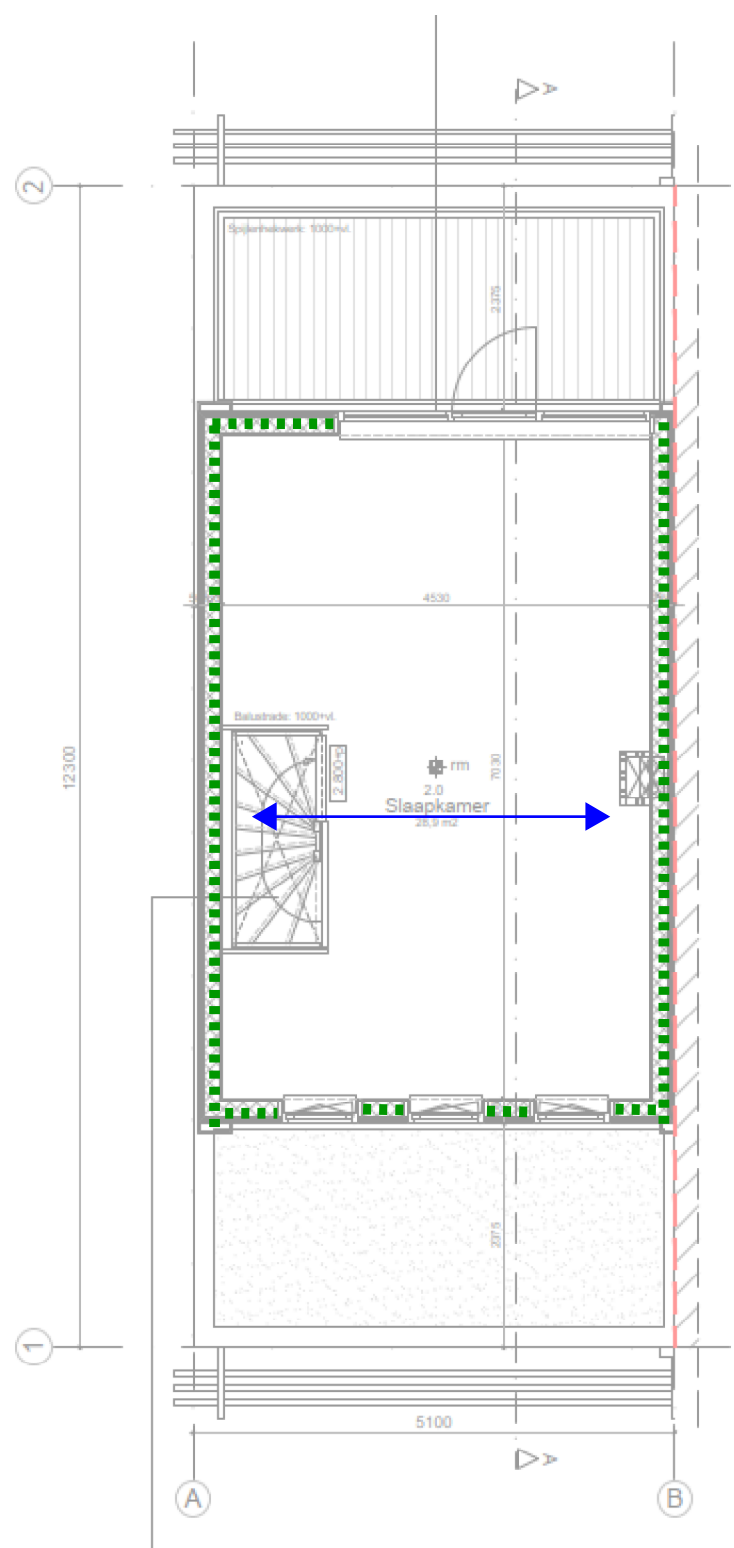

CONSTRUCTIE 3E VERDIEPING

- HSB-wand 38x184 hoh 610
1x vzv multiplex D 10 mm nagels 2.8x40 hoh 150
- ↔ Balklaag 71x196 hoh 610 mm

Renvooi hout

- bij balkaansluitingen balkschoenen toepassen
- houtkwaliteit: C24
- kwaliteit beschot: CE2+
- beschot verzorgt schijfwerking, underlayment toepassen

Renvooi staal

- alle stalen onderdelen in aanraking met de buitenlucht/spouw dienen thermisch verzinkt te worden
- staalconstructie te voorzien van ankers, bouten, strippen, schotten, wapening, bevestigen voor balklagen
- staalkwaliteit: S235, kokers S275
- boutkwaliteit: 8.8
- ankerkwaliteit: 4.6
- berekening staalverbindingen door staalleverancier te verzorgen. Berekeningen ter goedkeuring opsturen naar 3BM Bouwtechniek

CONSTRUCTIE OVERZICHT

Dakopbouw M.C. Grimberg-huijserstraat 43
Rotterdam

Opdrachtgever: Slappendel Bouw

Projectnr: 3090
Fase: UV
Auteur: M.D. Vroegindeweyj

Formaat: A2
Schaal: n.v.t.
1^e datum: 24-04-2026
Status:
Tekeningnr: CP-21

 **3bm**
Ingenieurs van oplossingen

3BM Cooperatie U.A.
Wattstraat 17
3335 LV Zwijndrecht

tel: 078 7400 250
info@3bm.co.nl
www.3bm.co.nl

