


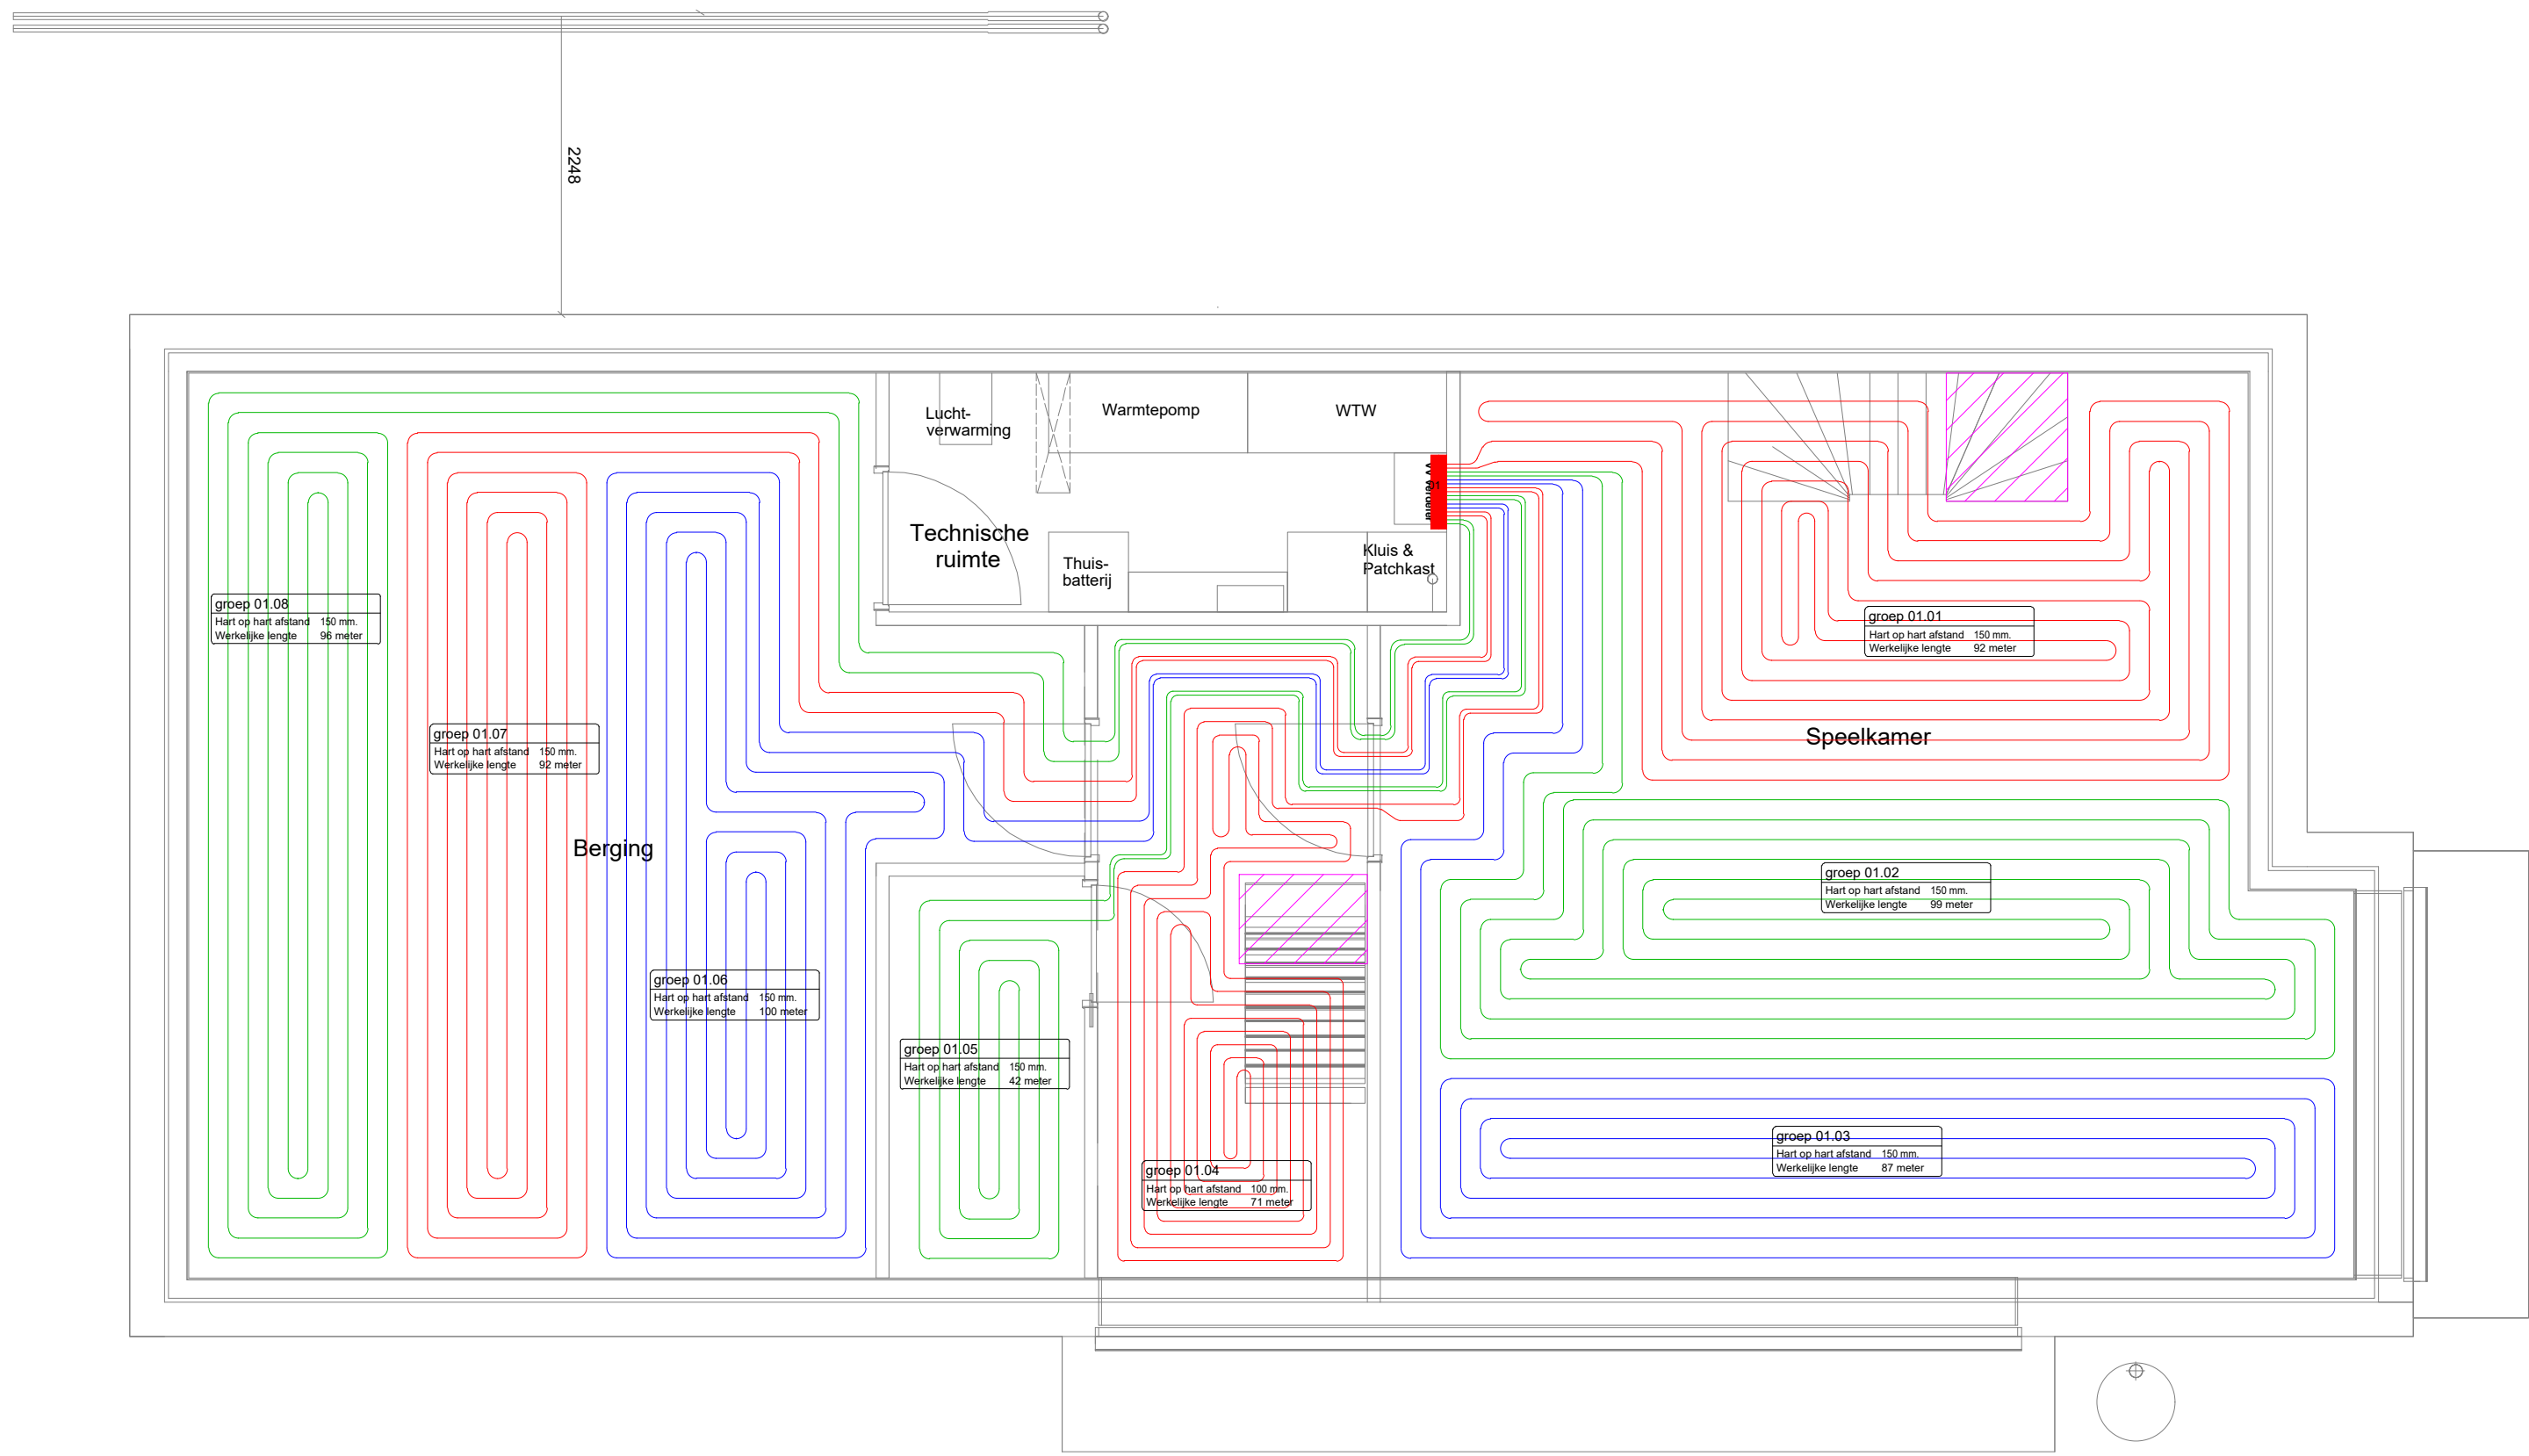


Kelder

Regelunit 01					Kunststof 8	
Leidingtype : PE-RT 16/2 mm					Primair drukverlies : 16.89 kPa.	
Afmetingen in mm : h = 400 b = 555 d = 145					Secundair drukverlies : 0 kPa.	
Bevestigingsmateriaal: Vlechten					Temperatuur traject : 30/30°C	
Gr.	Ruimte naam/Ruimtenummer	Ruimtetemperatuur(°C)	Transmissie(Watt)	Debiet(l/m)	Vloerafwerking	
01	Berging	18	558	1.85	Tapijt / parket	
02	Berging	18	600	1.98	Tapijt / parket	
03	Berging	18	527	1.75	Tapijt / parket	
04	Gang	18	284	0.93	Tapijt / parket	
05	Ontberooide Ruimte	18	255	0.83	Tapijt / parket	
06	Speelkamer	20	606	2	Tapijt / parket	
07	Speelkamer	20	558	1.85	Tapijt / parket	
08	Speelkamer	20	582	1.92	Tapijt / parket	

Overzicht Groepen		
Groepsnummer	H.O.H.	Lengte
groep 01.01	150 mm.	92 meter
groep 01.02	150 mm.	99 meter
groep 01.03	150 mm.	87 meter
groep 01.04	100 mm.	71 meter
groep 01.05	150 mm.	42 meter
groep 01.06	150 mm.	100 meter
groep 01.07	150 mm.	92 meter
groep 01.08	150 mm.	96 meter
Verdeler 01	Totaal:	679 meter


Voorverwarmingsbus:		PE-RT 20x2 mm: -		PE-RT 18x2 mm: -		PE-RT 16x2 mm: 679 meter		PE-RT 14x2 mm: -		
Nr. Type:	Bevestigingsmateriaal:	Nr. Type:	Bevestigingsmateriaal:	Nr. Type:	Bevestigingsmateriaal:	Nr. Type:	Bevestigingsmateriaal:	Nr. Type:	Bevestigingsmateriaal:	
1	Kunststof 8	8		15		22				
2	Vlechten	9		16		23				
3		10		17		24				
4		11		18		25				
5		12		19		26				
6		13		20		27				
7		14		21		28				
Wijz. Datum:	Tekenaar:	Omschrijving van de wijziging:								
1										
2										
3										
4										
5										
6										
7										
8										
Project naam		: Woning B. van Dorp						Ter Goedkeuring		
Project adres		: Kralingseweg 370								
Project postcode/plaats										
Projectnummer klant										
Tekenaar		: GCH		Formaat : A1		Projectnummer				:
Tekendatum		: 23-03-2026						Bladnummer		: W-01
Bouwkundige tekening		: 1368-Kelder.pdf						Verdieping		: Kelder
Datum bouw. tekening								Schaal		: 1:50 Type :
								Gebouw		:
								Bouwnummer(s)		:

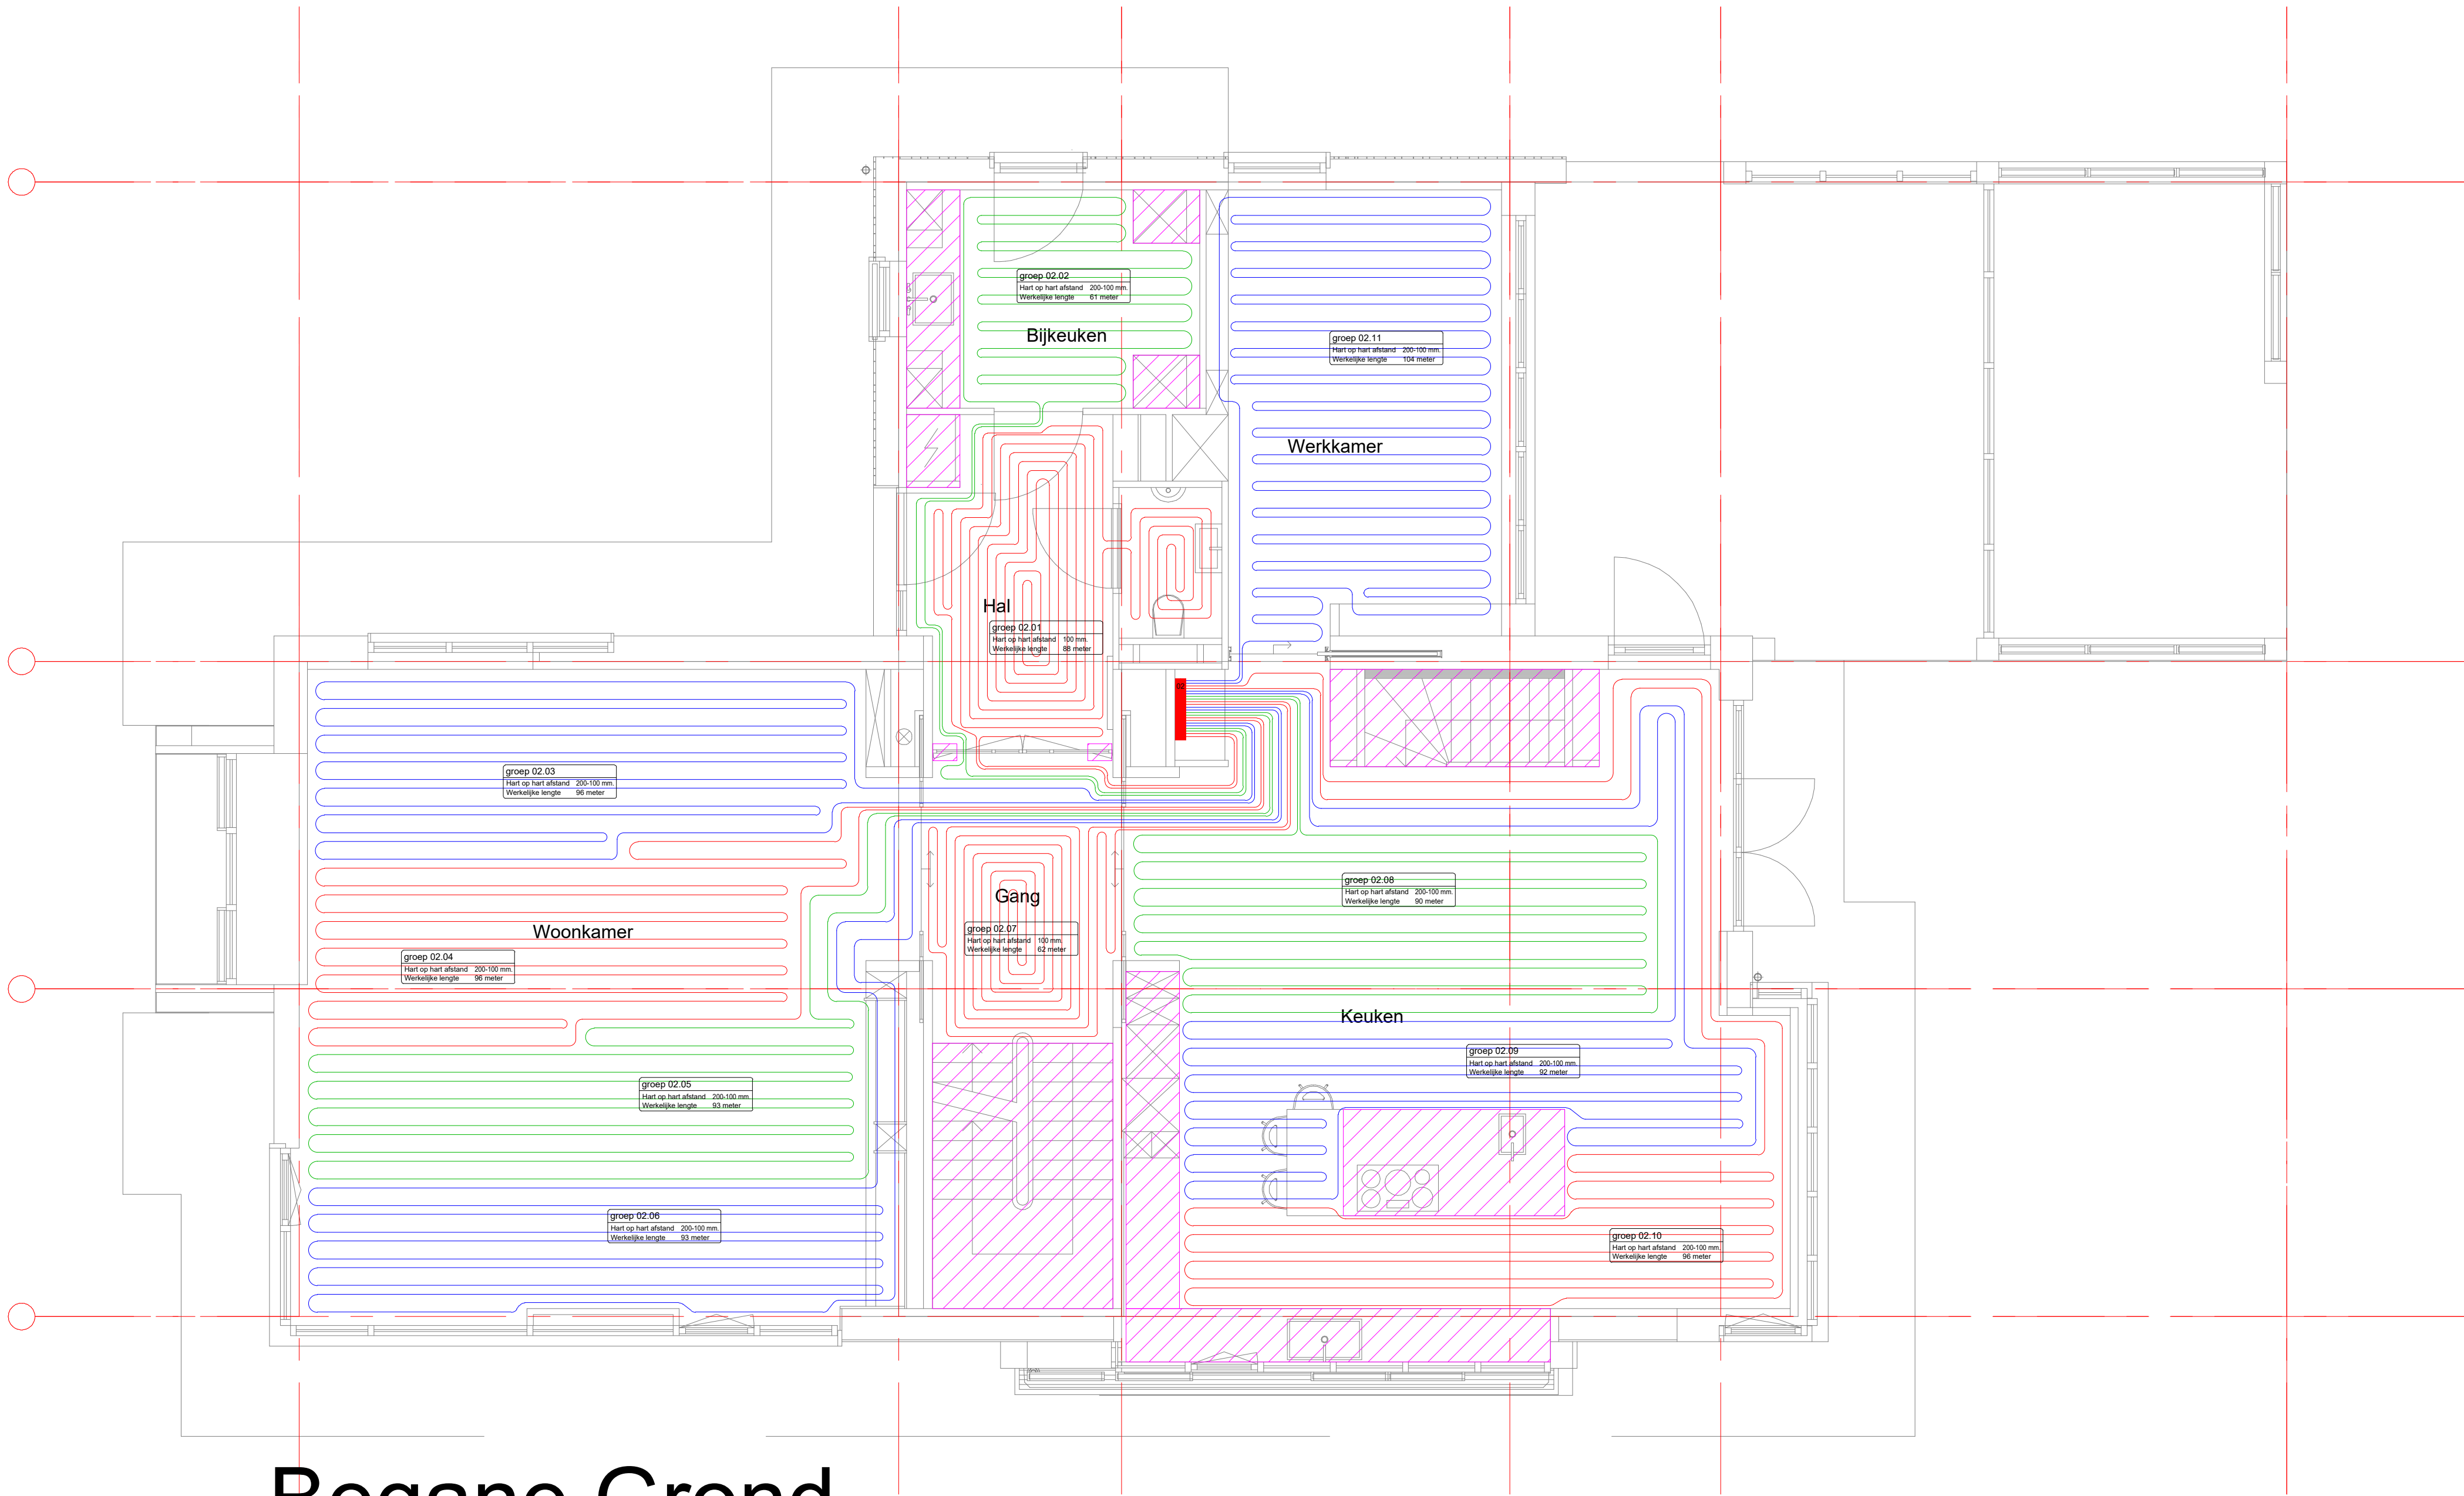


Begane Grond

Regelunit 02					Kunststof 11	
Leidingtype : PE-RT 18x2 mm					Primair drukverlies : 19,83 kPa.	
Afmetingen in mm : h = 400 b = 600 d = 145					Secundair drukverlies : 0 kPa.	
Bevestigingsmateriaal : Tackeren/Vlechten					Temperatuur traject : 35/30°C	
Gr.	Ruimte naam/Ruimtenummer	Ruimtetemperatuur(°C)	Transmissie(Watt)	Debiet(l/m)	Vloerafwerking	
01	Hal	18	523	1,73	Tapijl / parket	
02	Bijkeuken	18	471	1,55	Tapijl / parket	
03	Woonkamer	22	533	1,77	Tapijl / parket	
04	Woonkamer	22	535	1,77	Tapijl / parket	
05	Woonkamer	22	530	1,75	Tapijl / parket	
06	Woonkamer	22	530	1,75	Tapijl / parket	
07	Gang	18	369	1,22	Tapijl / parket	
08	Keuken	22	536	1,77	Tapijl / parket	
09	Keuken	22	538	1,78	Tapijl / parket	
10	Keuken	22	540	1,78	Tapijl / parket	
11	Werkkamer	22	550	1,82	Tapijl / parket	

Overzicht Groepen		
Groepsnummer	H.O.H.	Lengte
groep 02.01	100 mm.	88 meter
groep 02.02	200-100 mm.	61 meter
groep 02.03	200-100 mm.	96 meter
groep 02.04	200-100 mm.	96 meter
groep 02.05	200-100 mm.	93 meter
groep 02.06	200-100 mm.	93 meter
groep 02.07	100 mm.	62 meter
groep 02.08	200-100 mm.	90 meter
groep 02.09	200-100 mm.	92 meter
groep 02.10	200-100 mm.	96 meter
groep 02.11	200-100 mm.	104 meter
Verdelers 02	Totaal:	971 meter

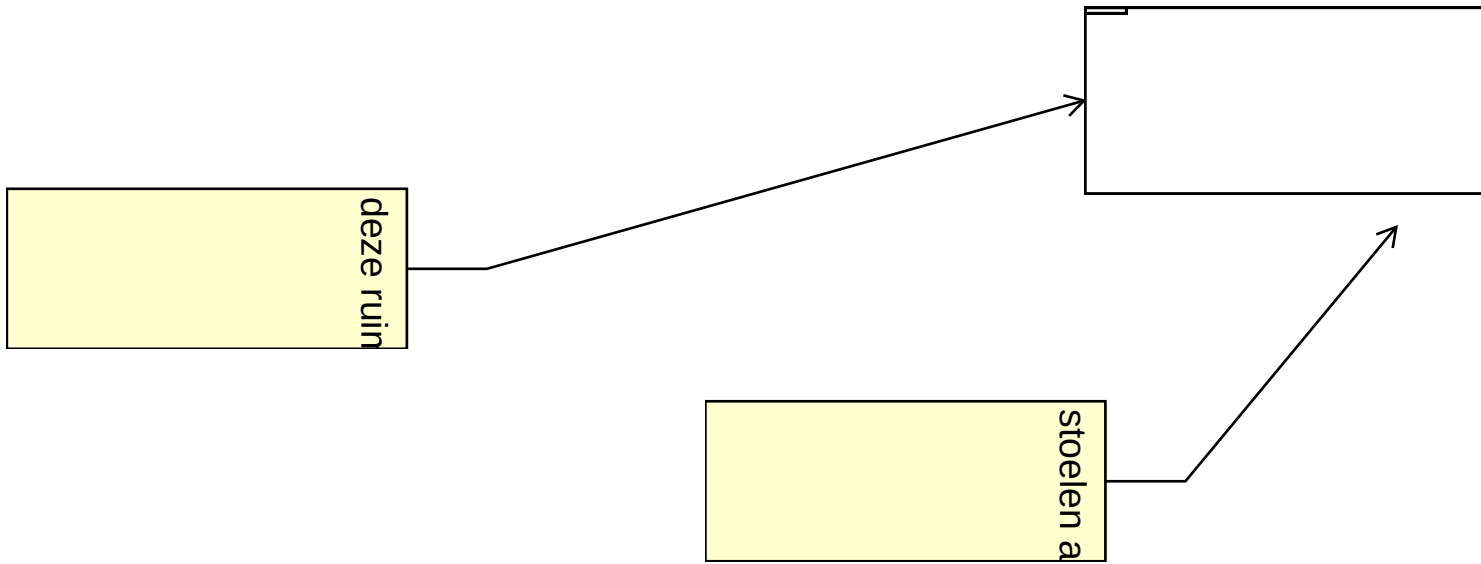

Vloerverwarmingsbuis		PE-RT 20x2 mm. -		PE-RT 18x2 mm. -		PE-RT 16x2 mm. 971 meter		PE-RT 14x2 mm. -			
Nr.	Type:	Bevestigingsmateriaal:	Nr.	Type:	Bevestigingsmateriaal:	Nr.	Type:	Bevestigingsmateriaal:	Nr.	Type:	Bevestigingsmateriaal:
1		8			15			22			
2	Kunststof 11	Tackeren/Vlechten	9		16			23			
3			10		17			24			
4			11		18			25			
5			12		19			26			
6			13		20			27			
7			14		21			28			
Wijz.	Datum:	Tekenaar:	Omschrijving van de wijziging:								
1											
2											
3											
4											
5											
6											
7											
8											
Project naam						Ter Goedkeuring					
Project adres						Projectnummer					
Project postcode/plaats						Bladnummer					
Projectnummer klant						Verdieping					
Tekenaar						Schaal					
Tekendatum						Type					
Bouwkundige tekening						Gebouw					
Datum bouw. tekening						Bouwnummer(s)					
: Woning B. van Dorp											
: Kralingseweg 370											
: 2025-05-29_Kralingseweg 370_Update Beg.Gr.											

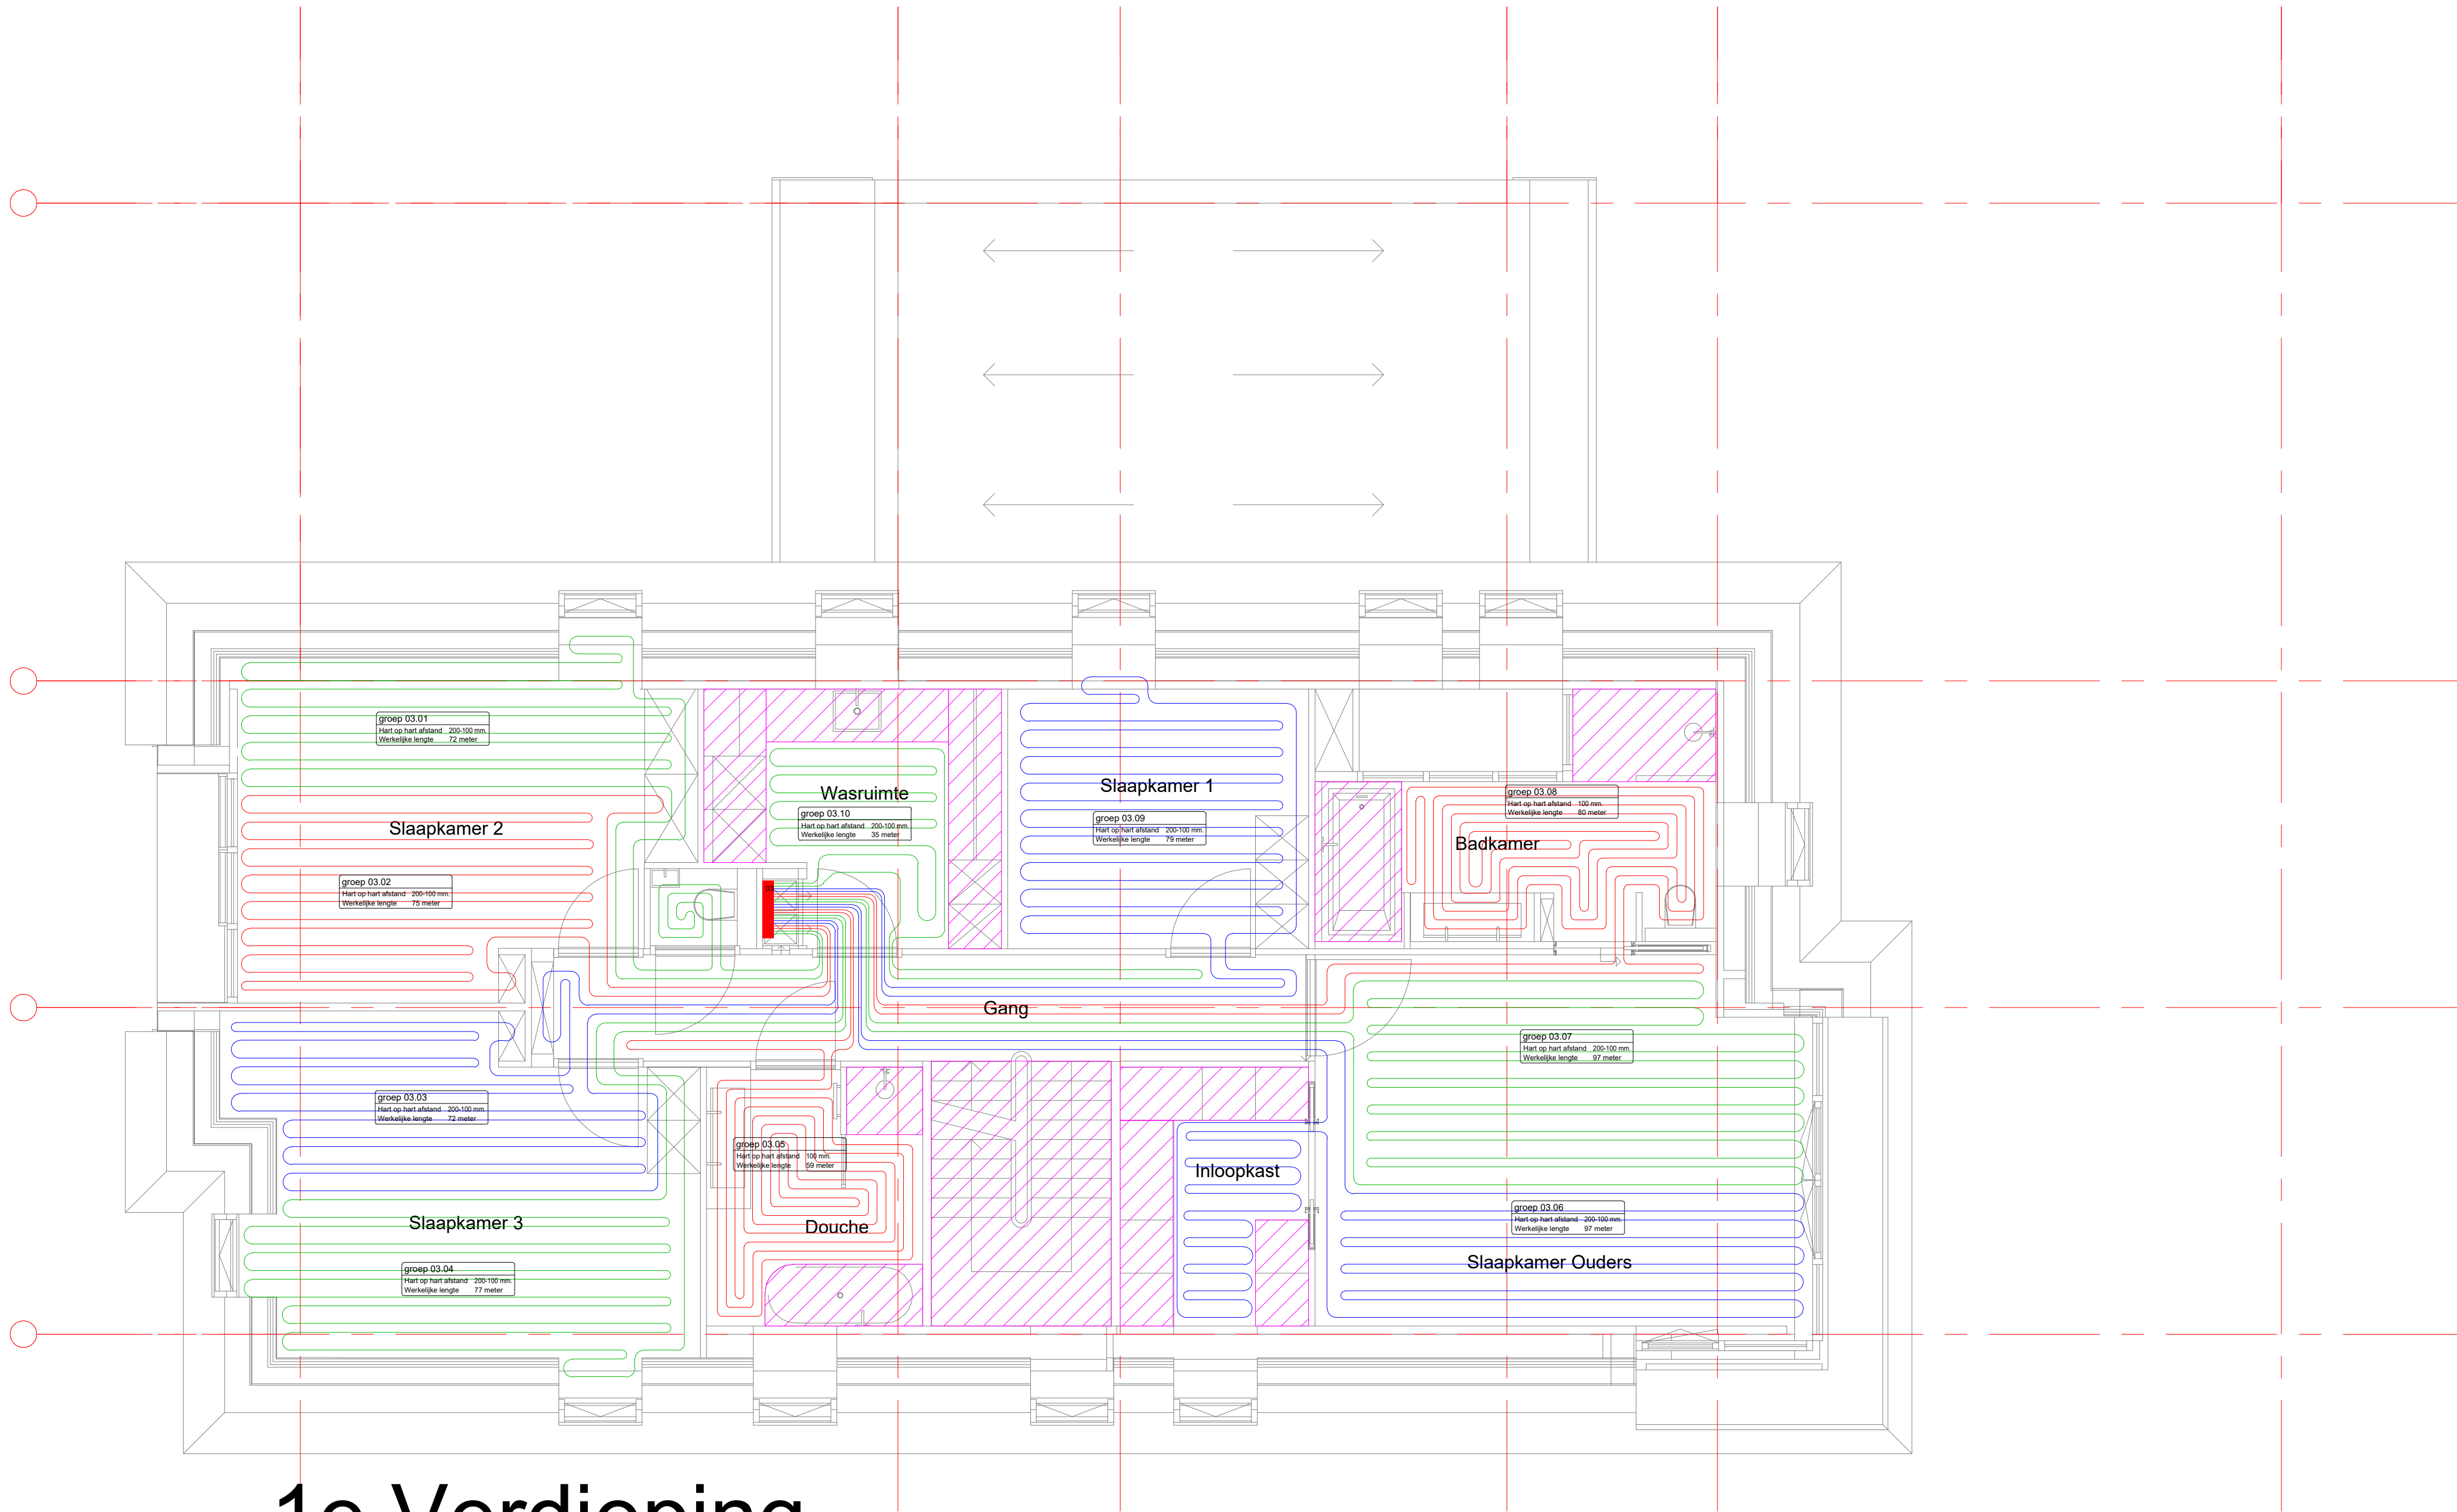


1e Verdieping

Regelunit 03					Kunststof 10			
Leidingtype : PE-RT 16/2 mm		Primair drukverlies : 18,32 kPa						
Afmetingen in mm : h = 400 b = 645 d = 145		Secundair drukverlies : 0 kPa						
Bevestigingsmateriaal : Tackeren/Vlechten		Temperatuur traject : 35/30°C						
Gr.	Ruimte naam/Ruimtenummer	Ruimtetemperatuur(°C)	Transmissie(Watt)	Debiet(l/m)	Vloerafwerking			
01	Slaapkamer 2	22	465	1.53	Tap(t) / parket			
02	Slaapkamer 2	22	484	1.6	Tap(t) / parket			
03	Slaapkamer 3	22	465	1.53	Tap(t) / parket			
04	Slaapkamer 3	22	497	1.65	Tap(t) / parket			
05	Douche	22	434	1.43	Steen / PVC			
06	Slaapkamer Ouders	22	592	1.96	Tap(t) / parket			
07	Slaapkamer Ouders	22	593	1.97	Tap(t) / parket			
08	Badkamer	22	589	1.96	Steen / PVC			
09	Slaapkamer 1	22	510	1.68	Tap(t) / parket			
10	Wasseruite	20	247	0.82	Tap(t) / parket			

Overzicht Groepen		
Groepsnummer	H.O.H.	Lengte
groep 03.01	200-100 mm.	72 meter
groep 03.02	200-100 mm.	75 meter
groep 03.03	200-100 mm.	72 meter
groep 03.04	200-100 mm.	77 meter
groep 03.05	100 mm.	59 meter
groep 03.06	200-100 mm.	97 meter
groep 03.07	200-100 mm.	97 meter
groep 03.08	100 mm.	80 meter
groep 03.09	200-100 mm.	79 meter
groep 03.10	200-100 mm.	35 meter
Verdeler 03	Totaal:	743 meter

Vloerverwarmingsbuis		PE-RT 20x2 mm. -	PE-RT 18x2 mm. -	PE-RT 16x2 mm. 743 meter	PE-RT 14x2 mm. -		
Nr.	Type:	Bevestigingsmateriaal:	Nr.	Type:	Bevestigingsmateriaal:	Nr.	Type:
1		8		15		22	
2		9		16		23	
3	Kunststof 10	Tackeren/Vlechten	10			24	
4			11			25	
5			12			26	
6			13			27	
7			14			28	
8				21			
Wijz.	Datum:	Tekenaar:	Omschrijving van de wijziging:				
1							
2							
3							
4							
5							
6							
7							
8							
Project naam			: Woning B. van Dorp			Ter Goedkeuring	
Project adres			: Kralingseweg 370				
Project postcode/plaats			:				
Projectnummer klant			:				
Tekenaar		: GCH	Formaat : A1				
Tekendatum		: 23-03-2026					
Bouwkundige tekening		: 2025-05-29_Kralingseweg 370_Update 1e Verd.					
Datum bouw. tekening		:					
					Projectnummer :		
					Bladnummer : W01		
					Verdieping : 1e Verdieping		
					Schaal : 1:50 Type :		
					Gebouw :		
					Bouwnummer(s) :		

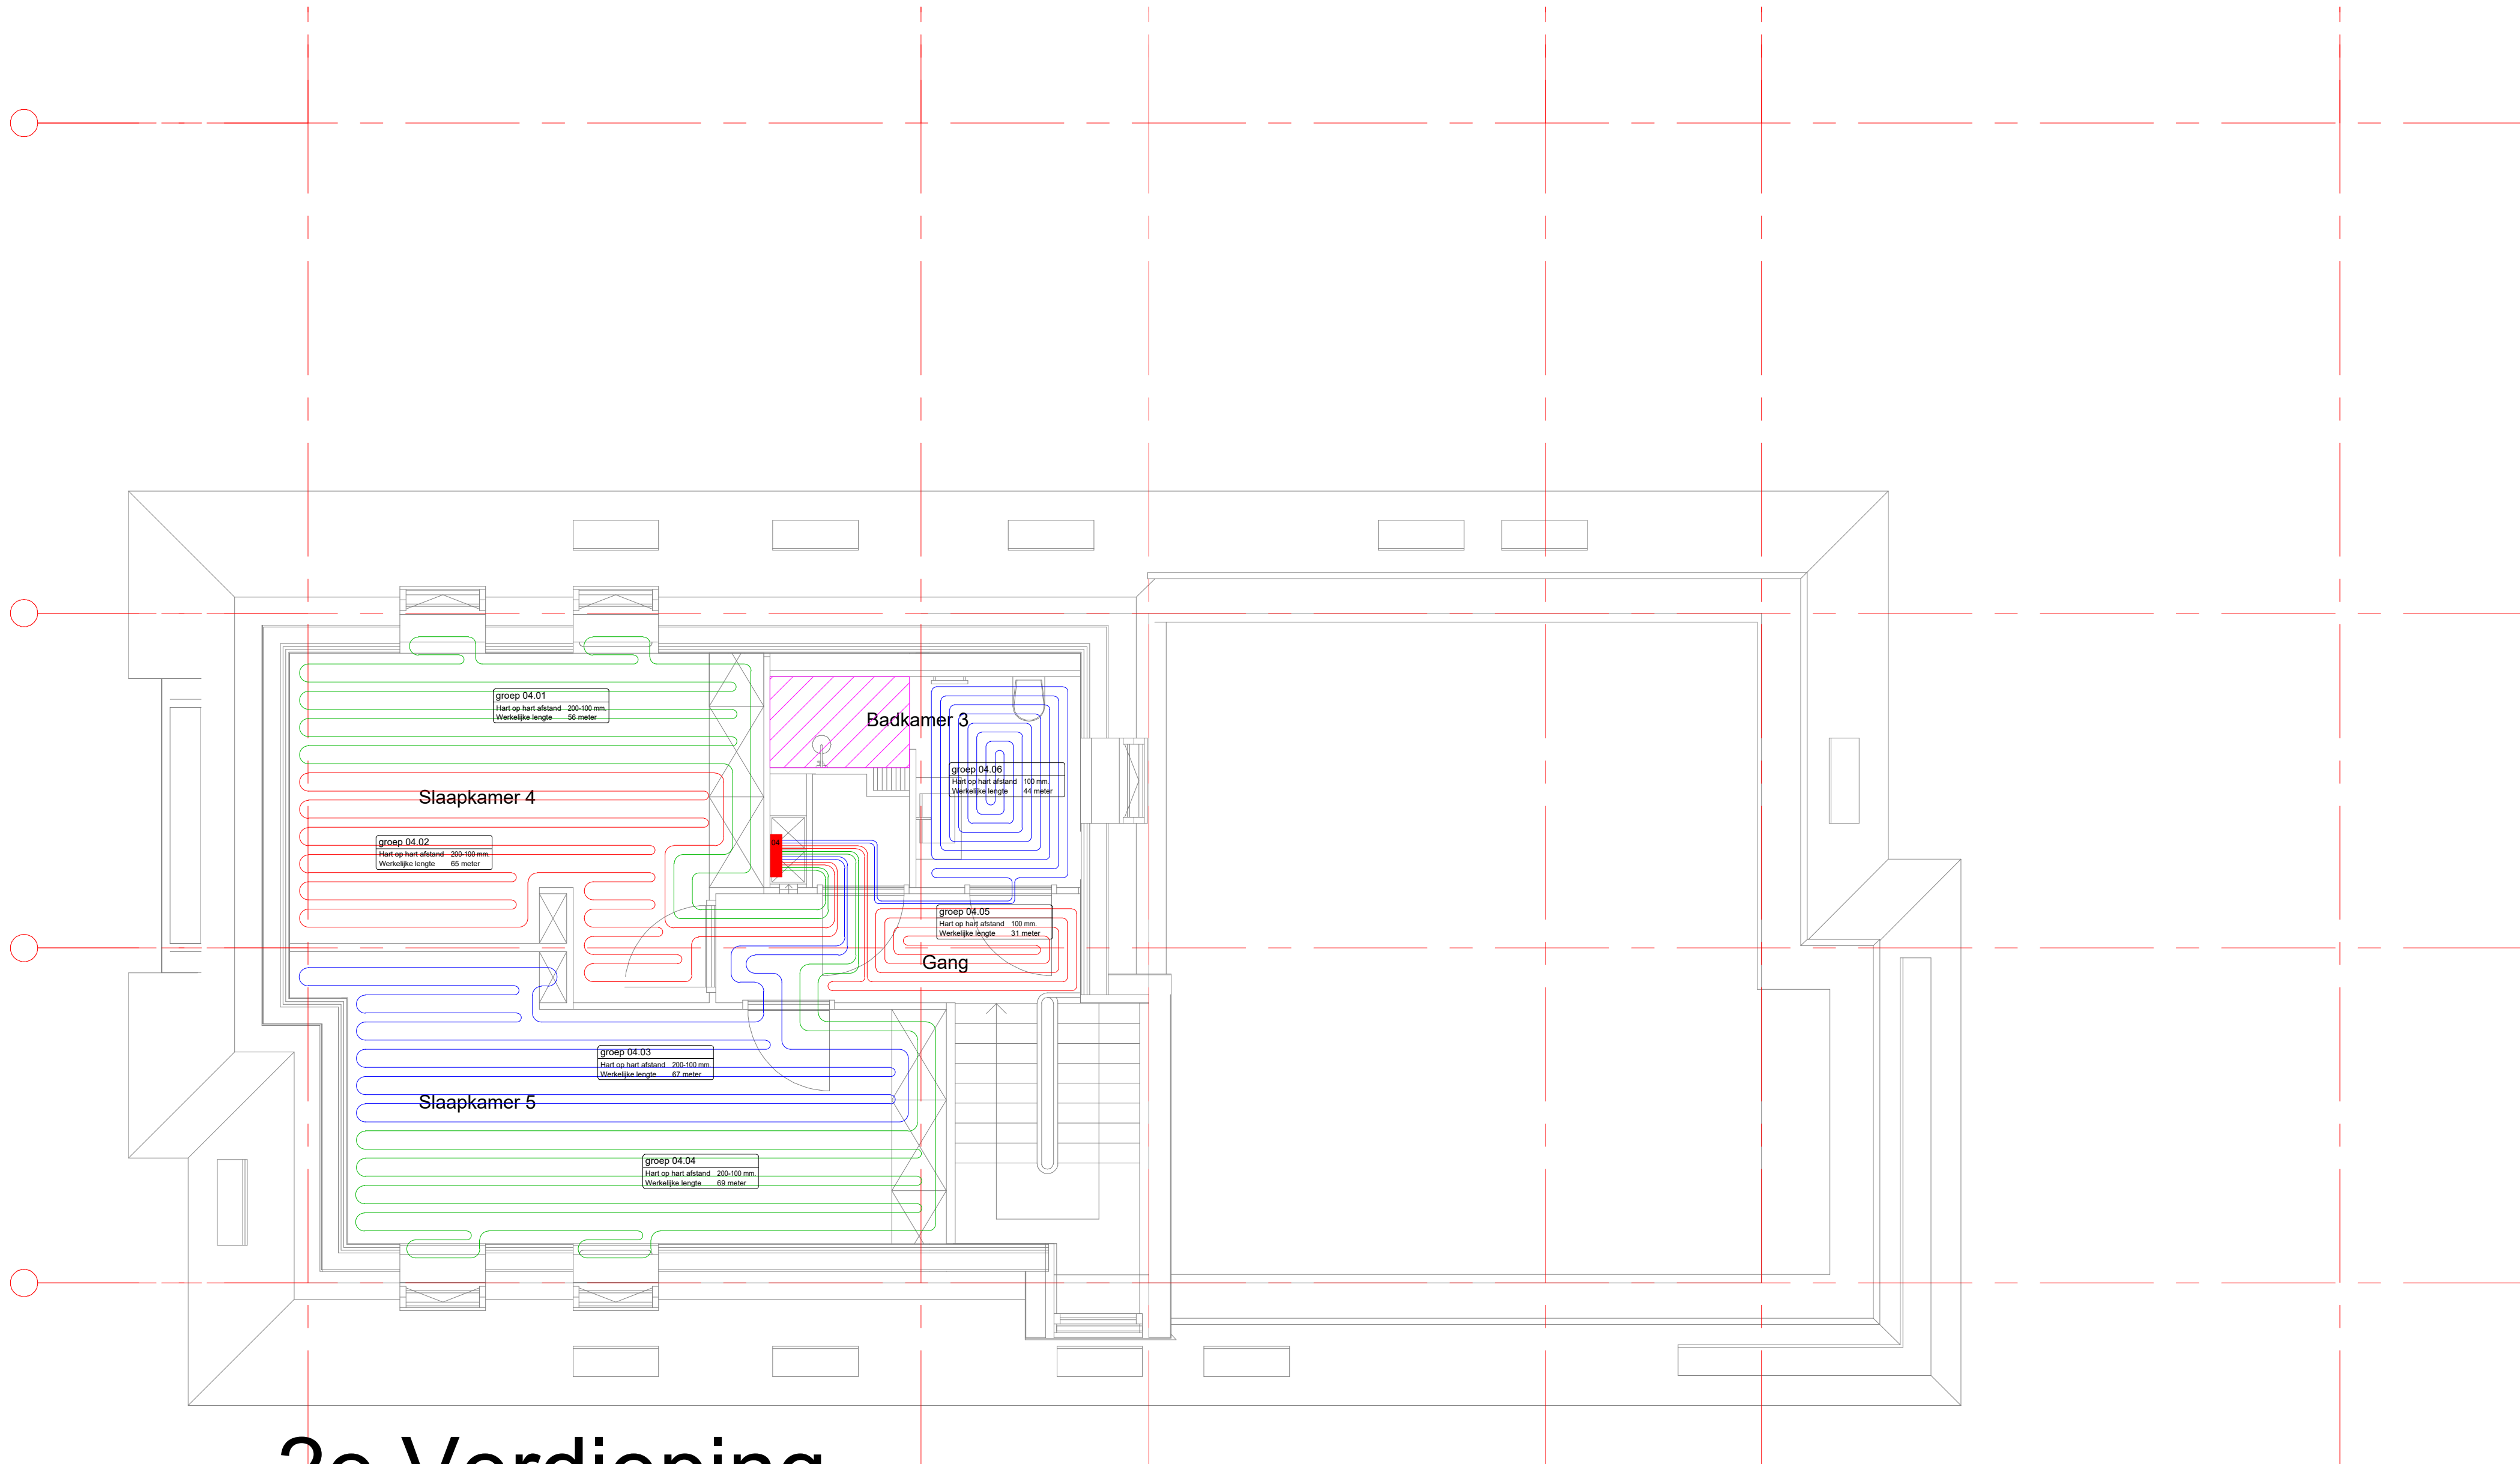

2e Verdieping

Regelunit 04				Kunststof 6			
Leidingtype : PE-RT 16x2 mm		Primair drukverlies : 5.58 kPa					
Afmetingen in mm : h = 400 b = 465 d = 145		Secundair drukverlies : 0 kPa					
Bevestigingsmateriaal: Tackeren/Vechten		Temperatuur traject : 35/30°C					
Gr.	Ruimte naam/Ruimtenummer	Ruimtetemperatuur(°C)	Transmissie(Watt)	Debiet(l/m)	Vloerafwerking		
01	Slaapkamer 4	22	362	1.2	Tap@ / parket		
02	Slaapkamer 4	22	420	1.38	Tap@ / parket		
03	Slaapkamer 5	22	435	1.43	Tap@ / parket		
04	Slaapkamer 5	22	446	1.47	Tap@ / parket		
05	Gang	18	184	0.82	Tap@ / parket		
06	Badkamer	22	324	1.07	Steen / PVC		

Overzicht Groepen		
Groepsnummer	H.O.H.	Lengte
groep 04.01	200-100 mm.	56 meter
groep 04.02	200-100 mm.	65 meter
groep 04.03	200-100 mm.	67 meter
groep 04.04	200-100 mm.	69 meter
groep 04.05	100 mm.	31 meter
groep 04.06	100 mm.	44 meter
Verdelers 04	Totaal:	332 meter

Vloerverwarmingsbuis		PE-RT 20x2 mm. :-		PE-RT 18x2 mm. :-		PE-RT 16x2 mm. 332 meter		PE-RT 14x2 mm. :-			
Nr.	Type:	Bevestigingsmateriaal:		Nr.	Type:	Bevestigingsmateriaal:		Nr.	Type:	Bevestigingsmateriaal:	
1		8				15				22	
2		9				16				23	
3		10				17				24	
4	Kunststof 6	Tackeren/Vechten		11		18				25	
5		12				19				26	
6		13				20				27	
7		14				21				28	
Wijz. Datum:		Tekenaar:		Omschrijving van de wijziging:							
1											
2											
3											
4											
5											
6											
7											
8											
Project naam						: Woning B. van Dorp					
Project adres						: Kralingseweg 370					
Project postcode/plaats											
Projectnummer klant											
Tekenaar						: GCH		Formaat : A1		Ter Goedkeuring Projectnummer : Bladnummer : W02 Verdieping : 2e Verdieping Schaal : 1:50 Type : Gebouw : Bouwnummer(s):	
Tekendatum						: 23-03-2026					
Bouwkundige tekening						: 2025-05-29_Kralingseweg 370_Update 2e Verd.					
Datum bouwkl. tekening											